

**СТРОИТЕЛЬСТВО ВОДОГРЕЙНОЙ КОТЕЛЬНОЙ 400  
ГКАЛ/ЧАС НА ТЕРРИТОРИИ ИВАНОВСКОЙ ТЭЦ-2  
(878.2023)**

Схемы электрические принципиальные электроснабжения электроприёмников от  
основного, дополнительного и резервного источников

878.2023-АСУ ТП.СБ.1

Том 42

|             |              |               |             |              |
|-------------|--------------|---------------|-------------|--------------|
| Име № подл. | Подп. и дата | Взамен инв. № | Име № дубл. | Подп. и дата |
|             |              |               |             |              |

Содержание

1 Схема АСУ ТП ВК F0CJU01 .....3

2 Схема АСУ Здания теплообменников N1CJU01 .....5

3 Схема АСУ ТП НАБ N2CJU01 .....6

4 Схема АСУ ГРП-1 E1CJU01 .....7

5 Схема АСУ ГРП-2 E2CJU01 .....8

6 Схема АСУ ЭТО E3CJU01 .....9



7 Схема серверного шкафа Z0CJU01.....10

8 Схема серверного шкафа Z0CJU02.....11

|             |  
|-------------|--|--------------|------|-----------|-------|-------|---|--|--|------|--|---------------|--|--|--|--|--|--|--|--|--|--|
| Име № подл. |  | Подп. и дата |      |           |       |       | Име № дубл.   |  |  |      |  | Взамен инв. № |  |  |  |  |  |  |  |  |  |  |
|             |  
|             |  
|             |  
|             |  |              |      |           |       |       | 878.2023-АСУ ТП.СБ.1   |  |  |      |  |               |  |  |  |  |  |  |  |  |  |  |
|             |  | Изм.         | Лист | № докум.  | Подп. | Дата  | Строительство водогрейной котельной 400 гкал/час на территории ивановской ТЭЦ-2.<br>Схемы электрические принципиальные электроснабжения электроприёмников от основного, дополнительного и резервного источников |  |  |      |  |               |  |  |  |  |  |  |  |  |  |  |
|             |  | Разраб.      |      | Чураков   |       | 08.25 |   |  |  |      |  |               |  |  |  |  |  |  |  |  |  |  |
|             |  | Пров.        |      | Агафонов  |       | 08.25 |   |  |  |      |  |               |  |  |  |  |  |  |  |  |  |  |
|             |  | Н. контр.    |      | Корепанов |       | 08.25 |   |  |  |      |  |               |  |  |  |  |  |  |  |  |  |  |
|             |  
|             |  |              |      |           |       |       | Стадия   |  |  | Лист |  | Листов        |  |  |  |  |  |  |  |  |  |  |
|             |  |              |      |           |       |       | Р   |  |  | 2    |  | 12            |  |  |  |  |  |  |  |  |  |  |
|             |  |              |      |           |       |       | ООО НПП «ЭСН»   |  |  |      |  |               |  |  |  |  |  |  |  |  |  |  |


1 Схема АСУ ТП ВК F0CJU01

начало

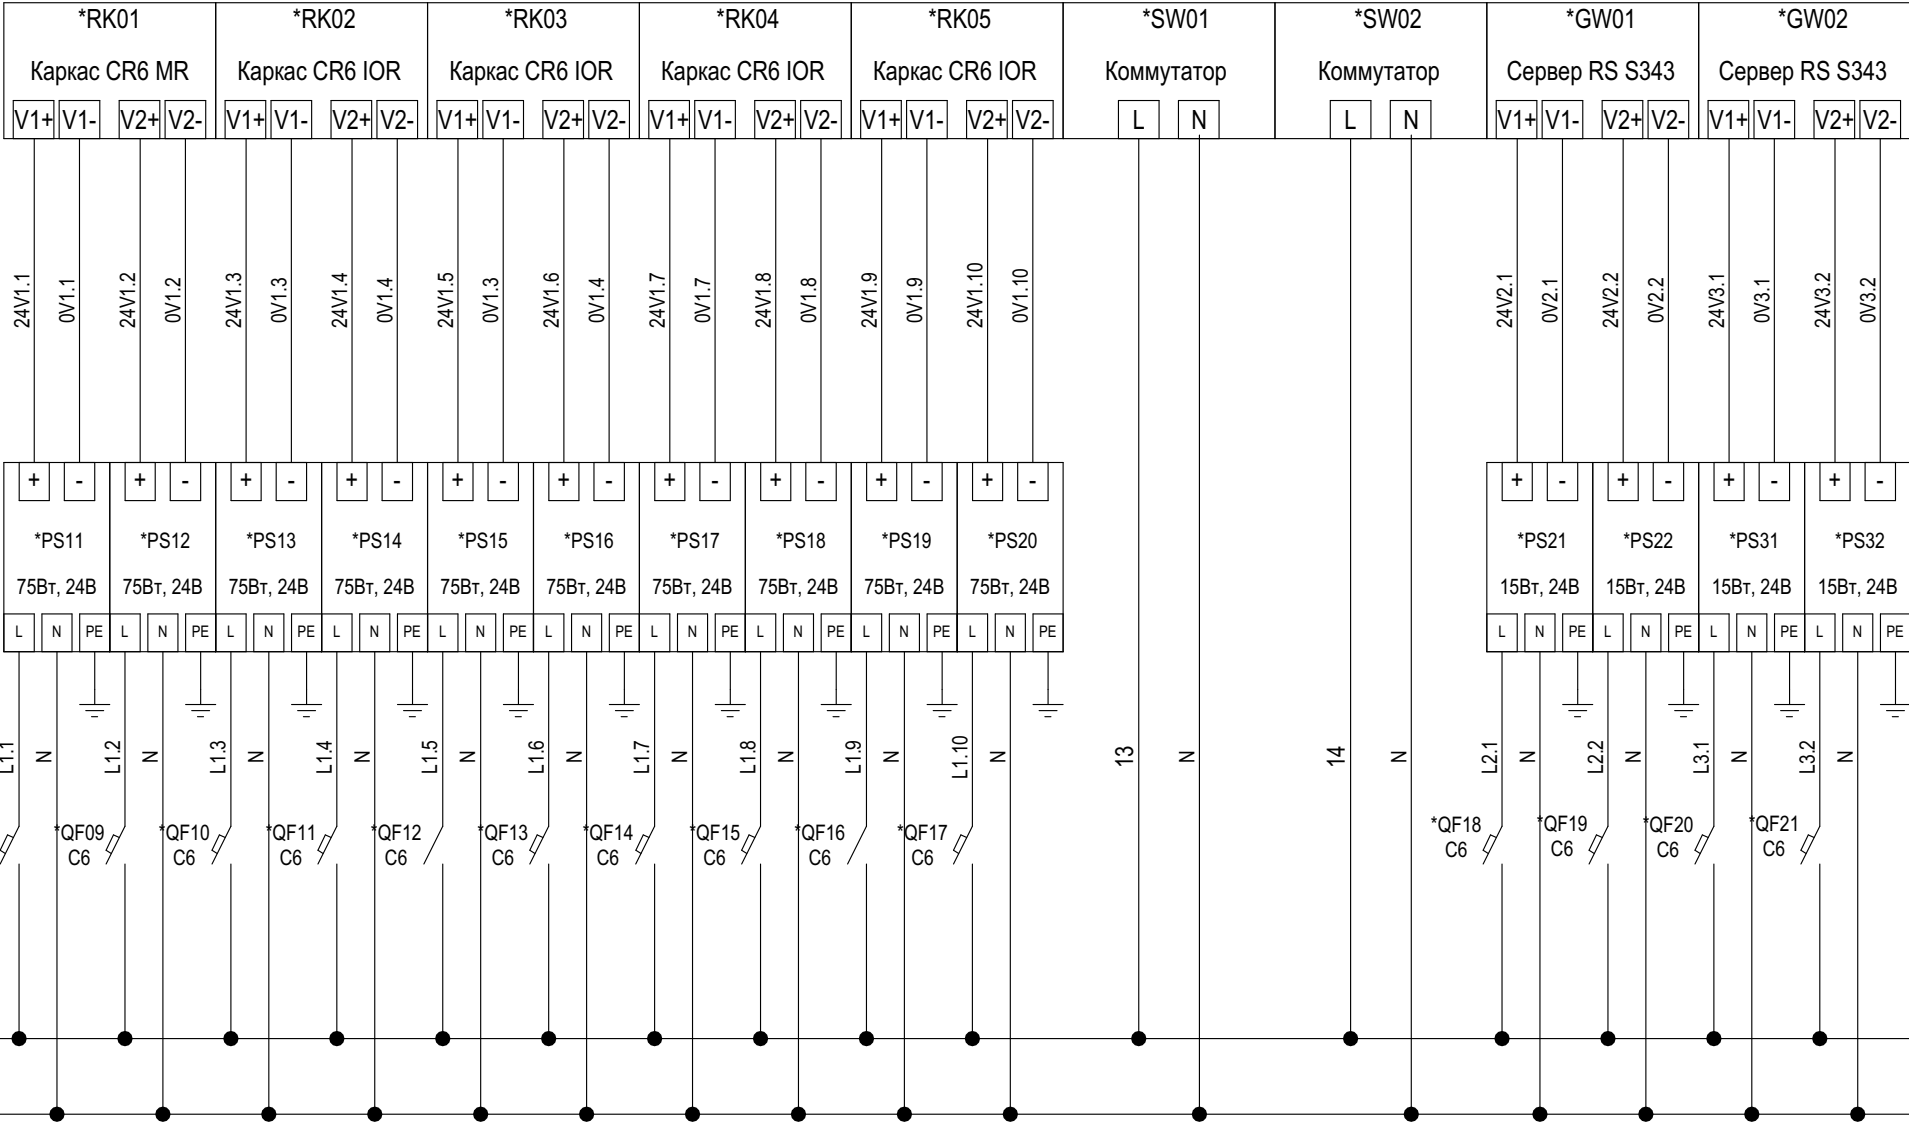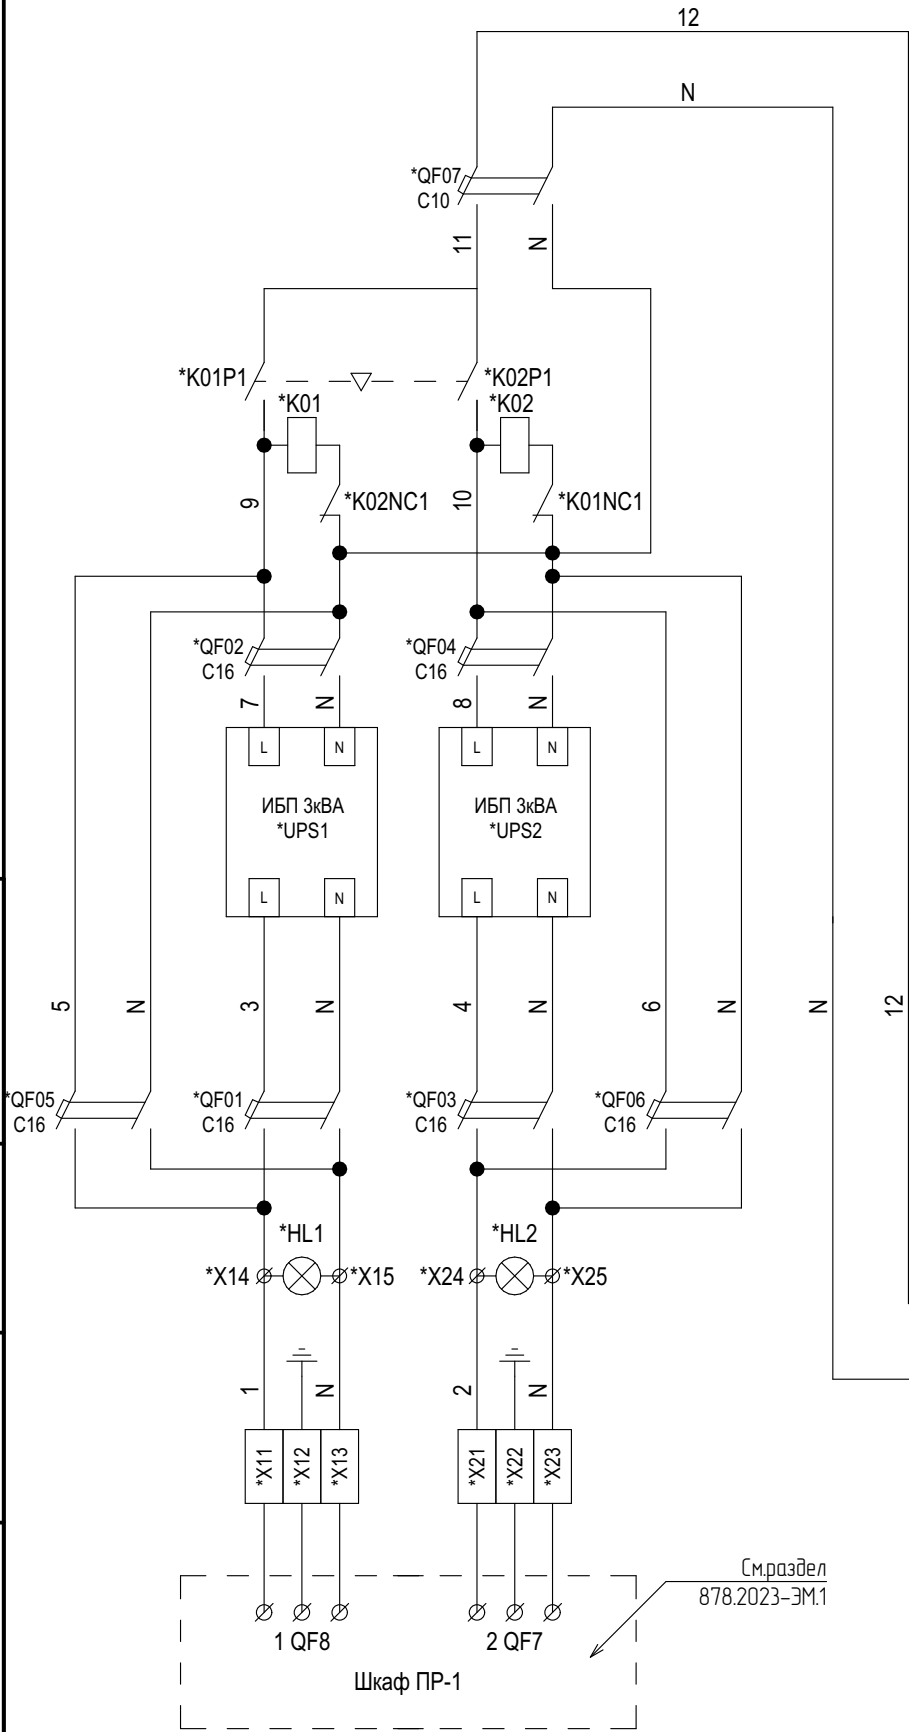

Примечание: \* - kks-код шкафа управления (F0CJU01);

продолжение

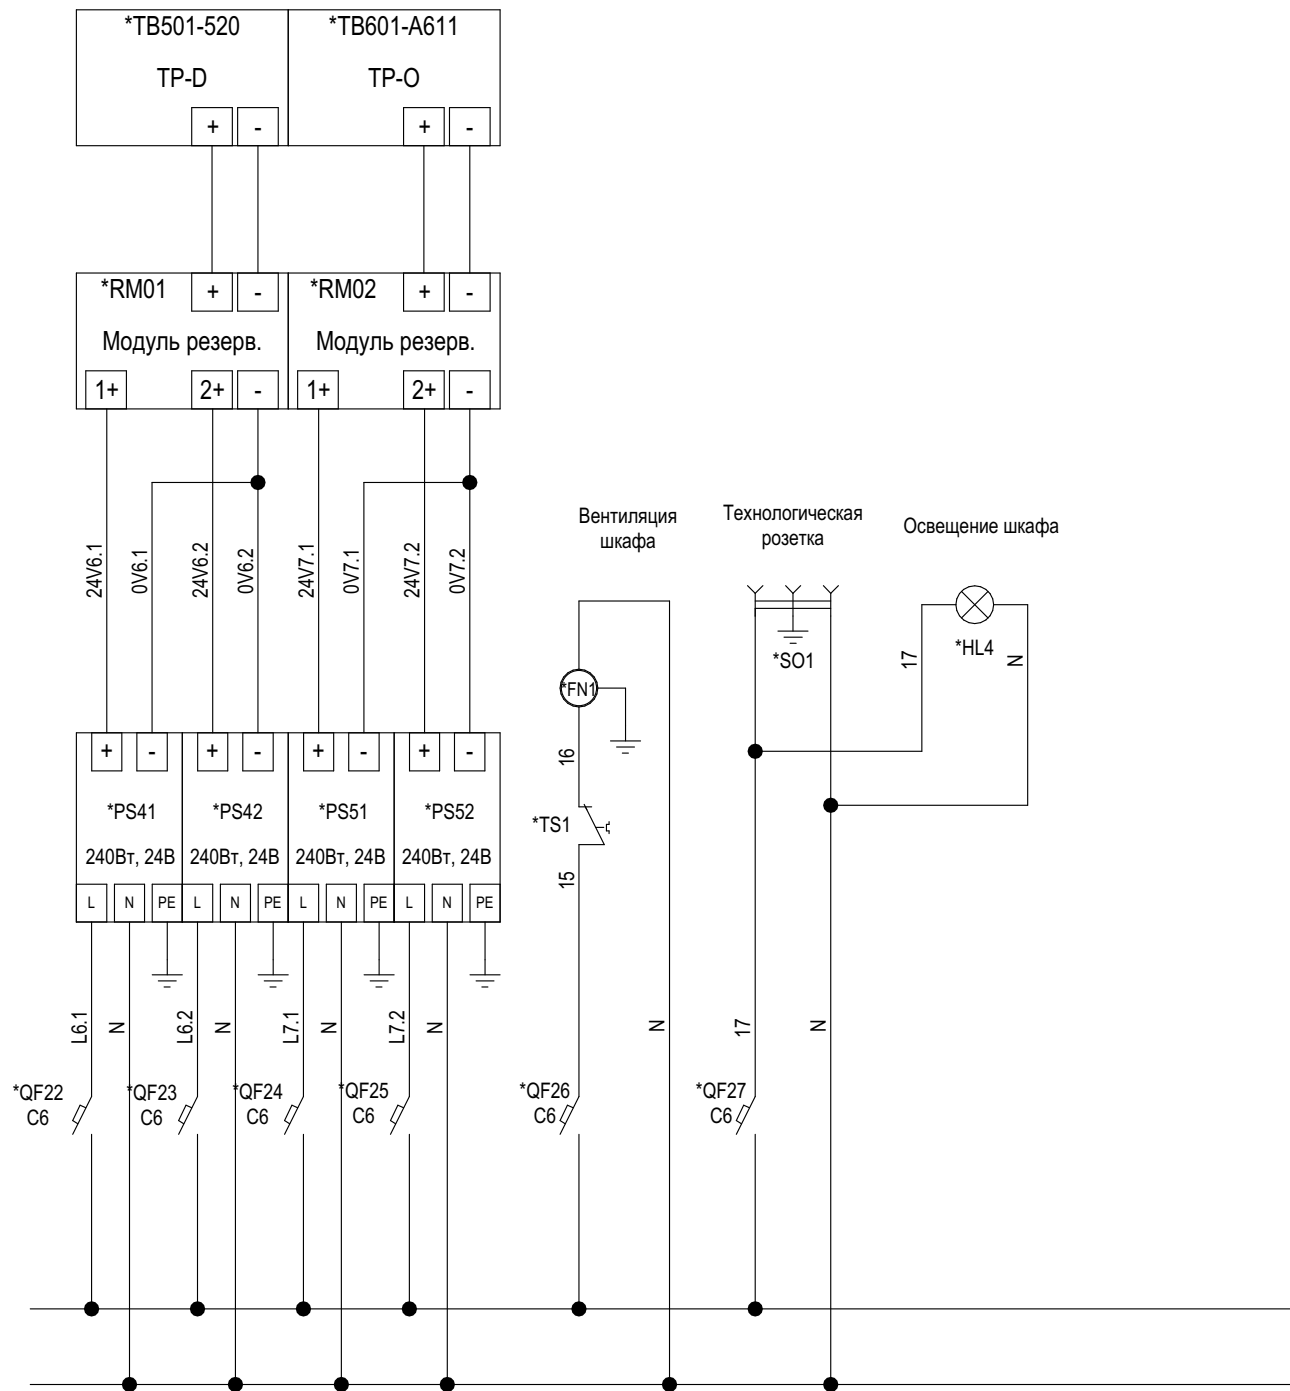


Примечание: \* – kks-код шкафа управления (F0CJU01);


|              |              |              |              |              |
|--------------|--------------|--------------|--------------|--------------|
| Инв. № подл. | Подп. и дата | Взам. инв. № | Инв. № дубл. | Подп. и дата |
|              |              |              |              |              |

2 Схема АСУ Здания теплообменников N1CJU01

|              |              |              |              |              |
|--------------|--------------|--------------|--------------|--------------|
| Изм. № подл. | Подп. и дата | Взам. инв. № | Изм. № дубл. | Подп. и дата |
|              |              |              |              |              |

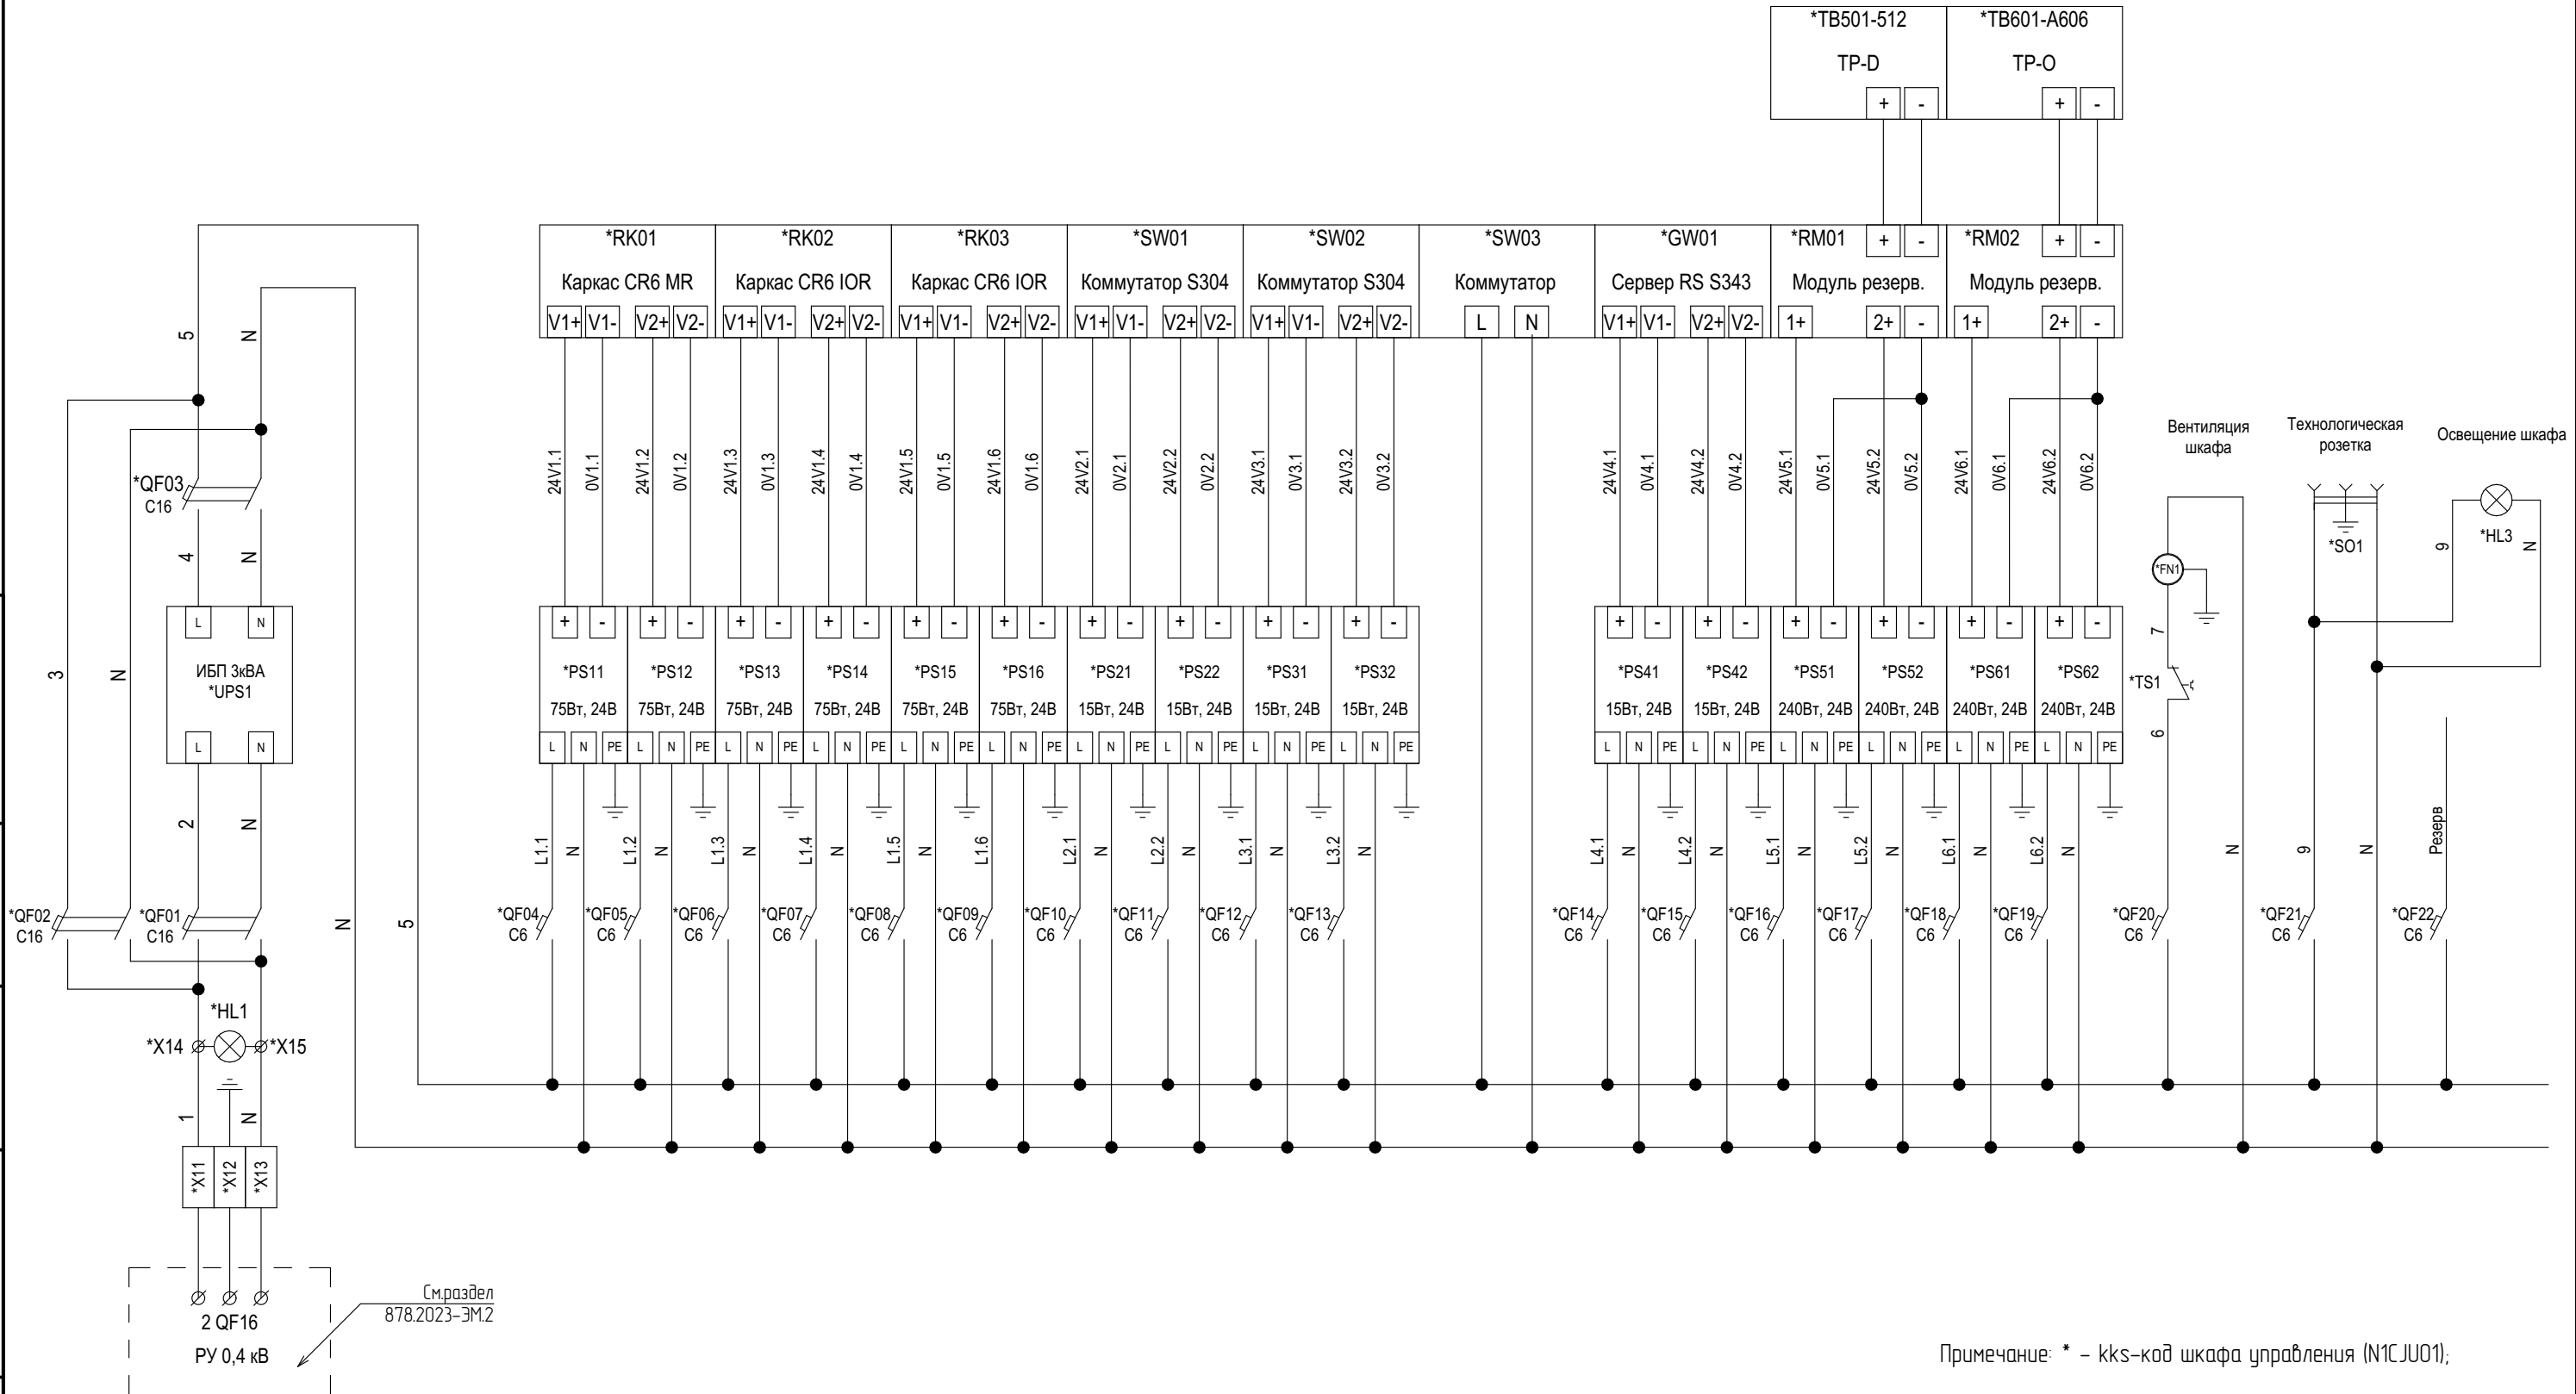

3 Схема АСУ ТП НАБ N2CJU01

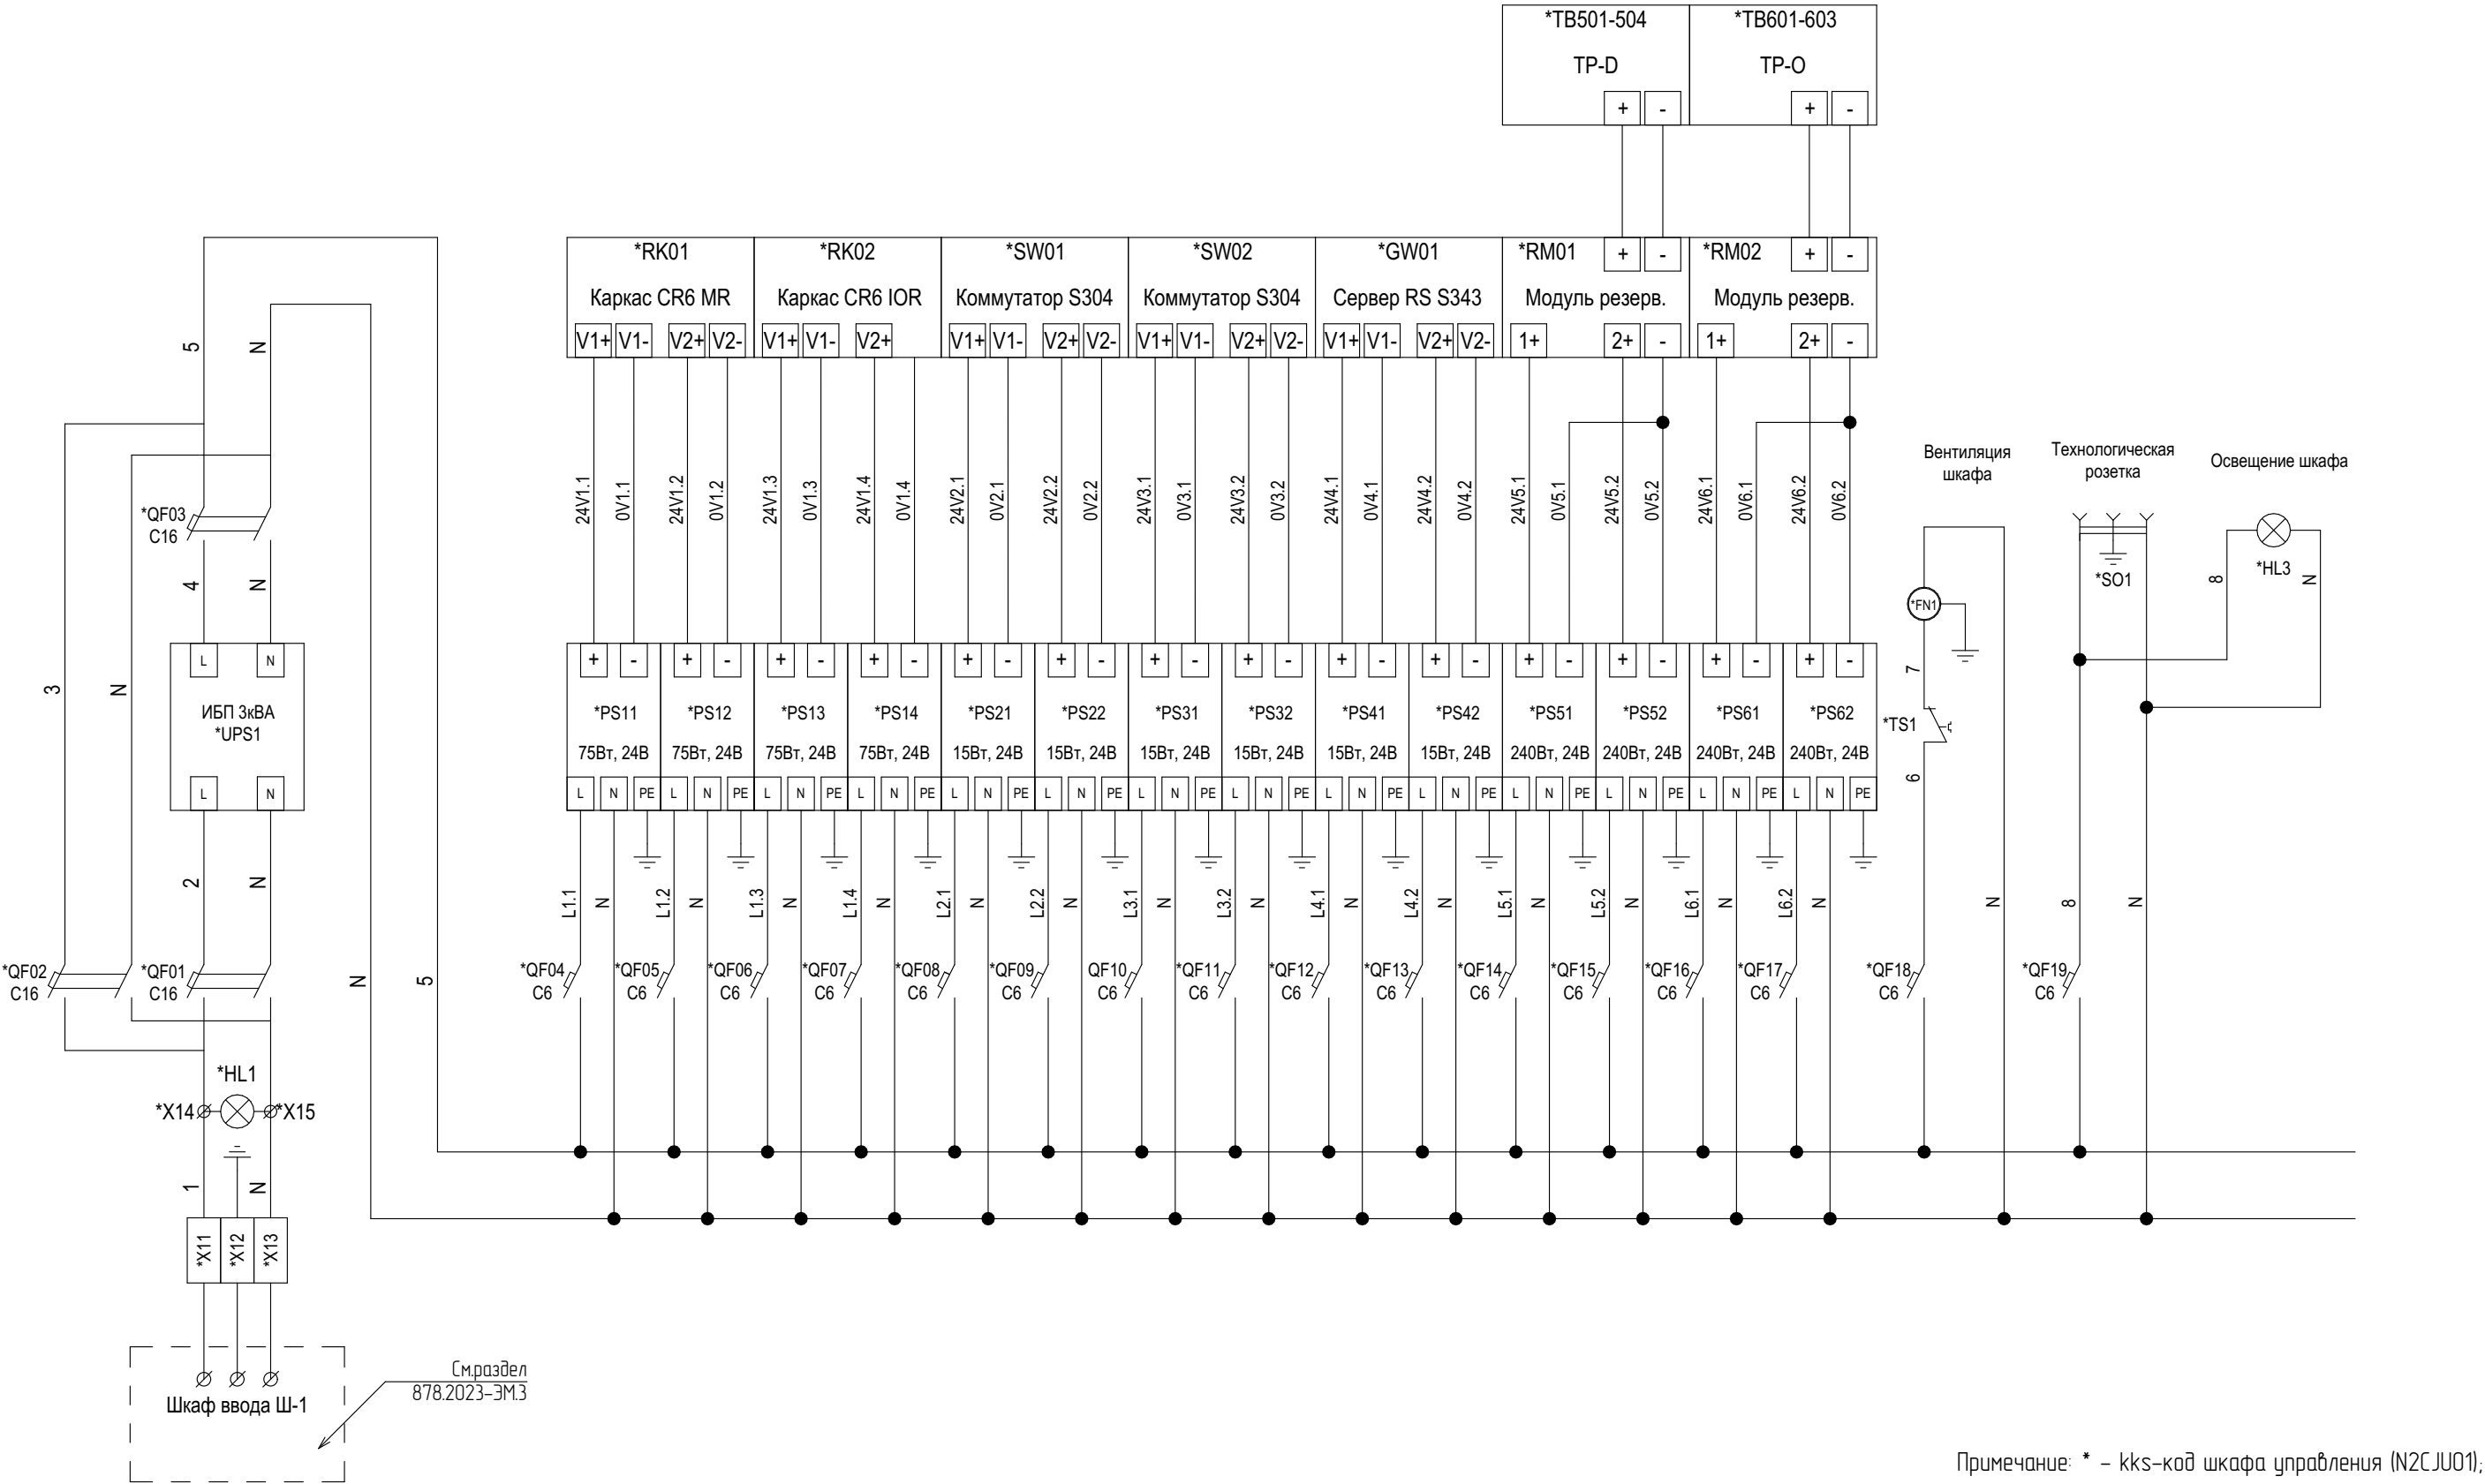


Примечание: \* - kks-код шкафа управления (N2CJU01);

|              |              |               |              |              |
|--------------|--------------|---------------|--------------|--------------|
| Изм. № подл. | Подп. и дата | Взамен шив. № | Име. № дубл. | Подп. и дата |
|              |              |               |              |              |

4 Схема АСУ ГРП-1 Е1СЈU01

|              |              |               |              |              |
|--------------|--------------|---------------|--------------|--------------|
| Изм. № подл. | Подп. и дата | Взамен шив. № | Изм. № дубл. | Подп. и дата |
|              |              |               |              |              |

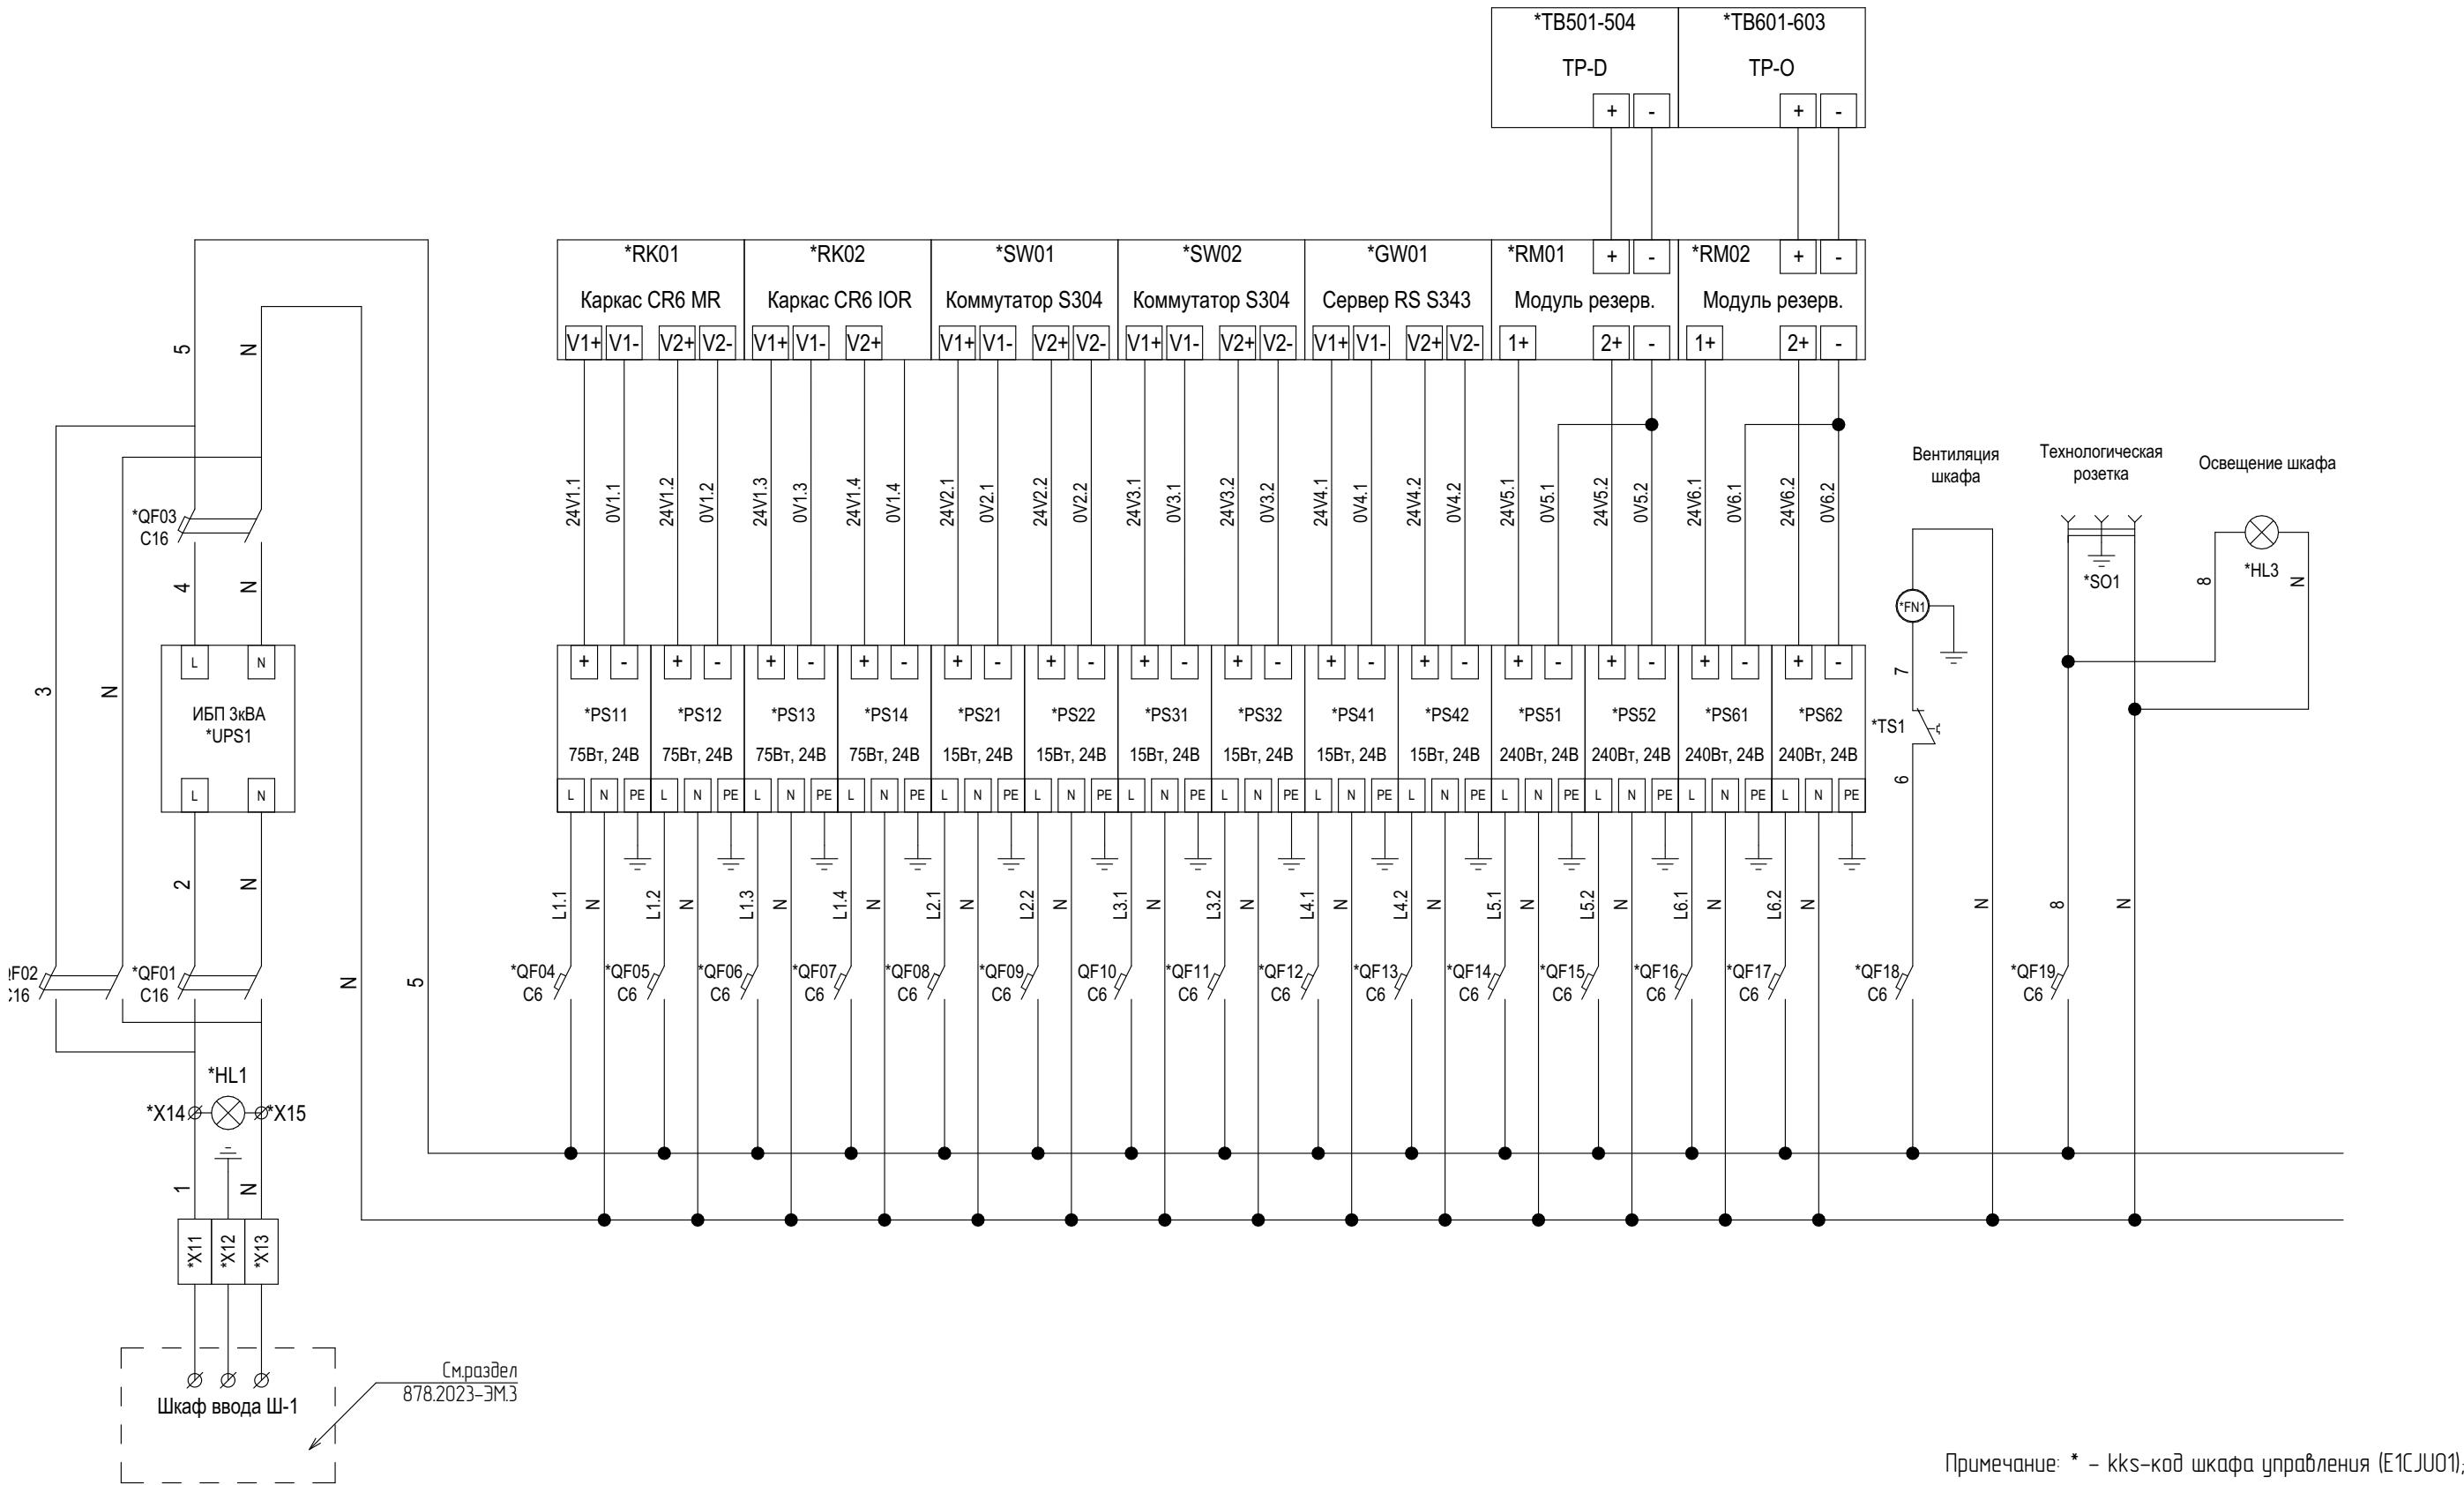


Примечание: \* - kks-код шкафа управления (Е1СЈU01);




5 Схема АСУ ГРП-2 Е2СЈU01

|              |              |              |              |              |
|--------------|--------------|--------------|--------------|--------------|
| Изм. № подл. | Подп. и дата | Взам. инв. № | Инв. № дубл. | Подп. и дата |
|              |              |              |              |              |

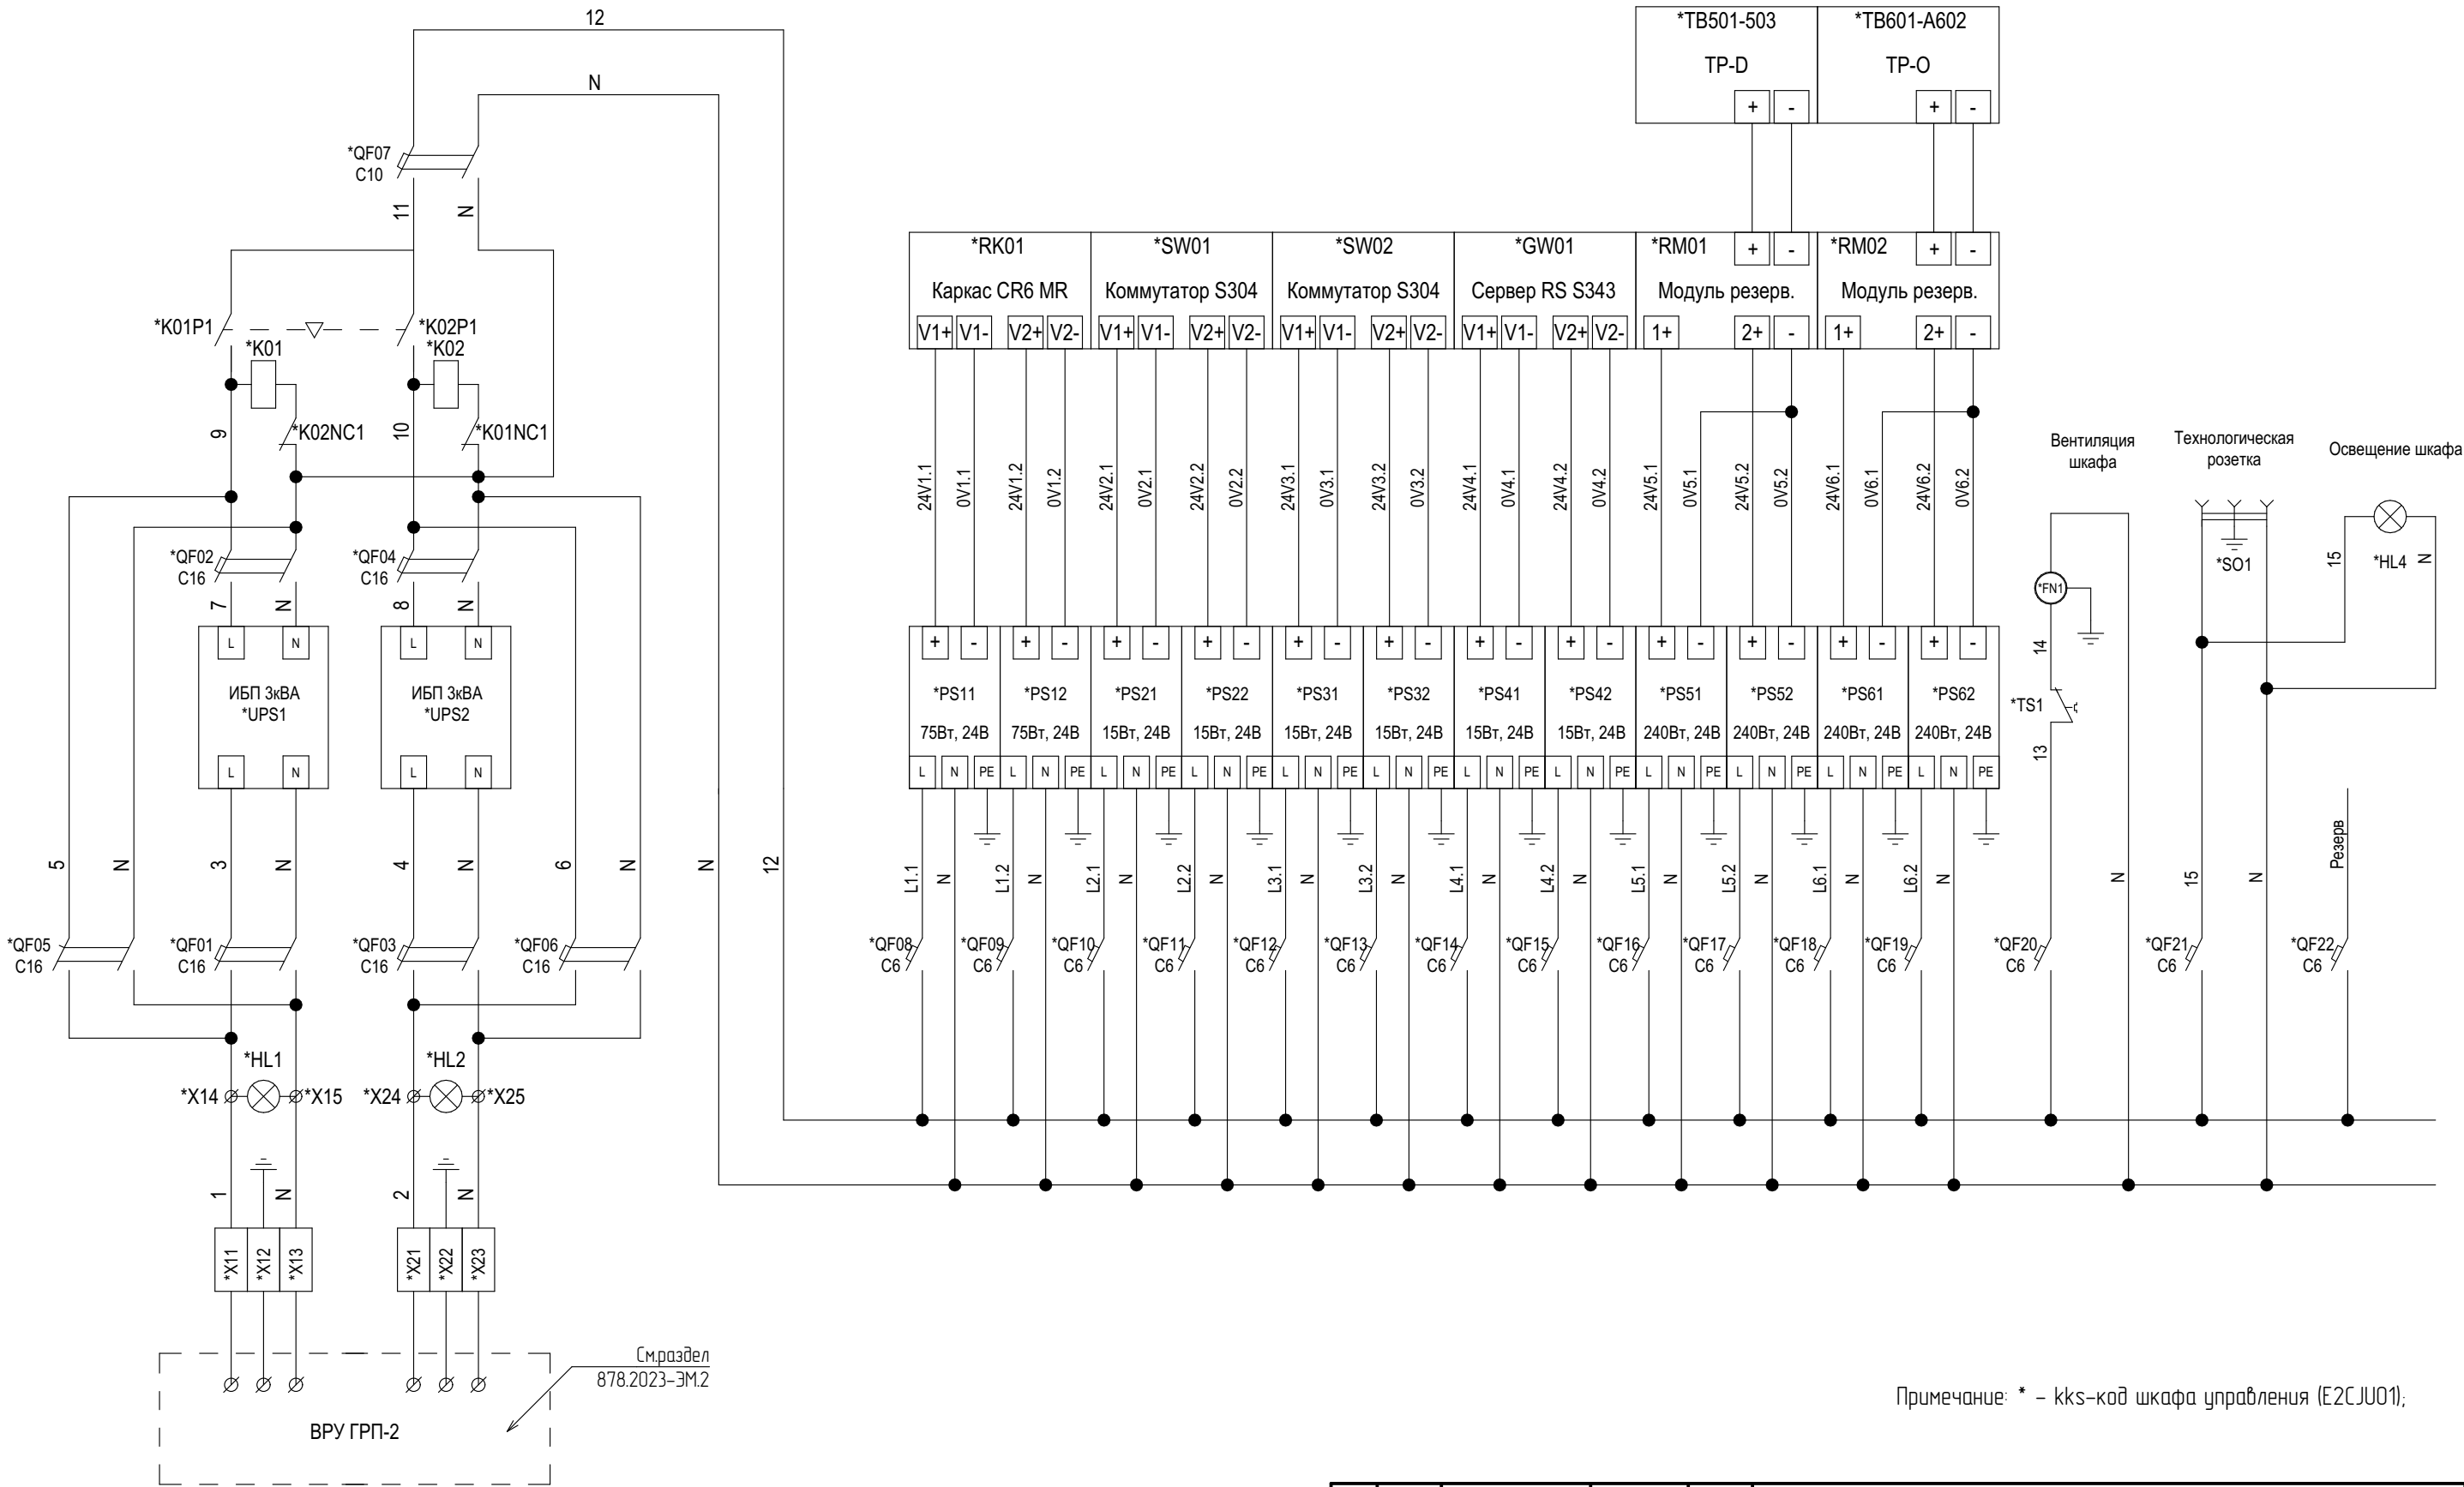



6 Схема АСУ ЭТО Е3СЈU01

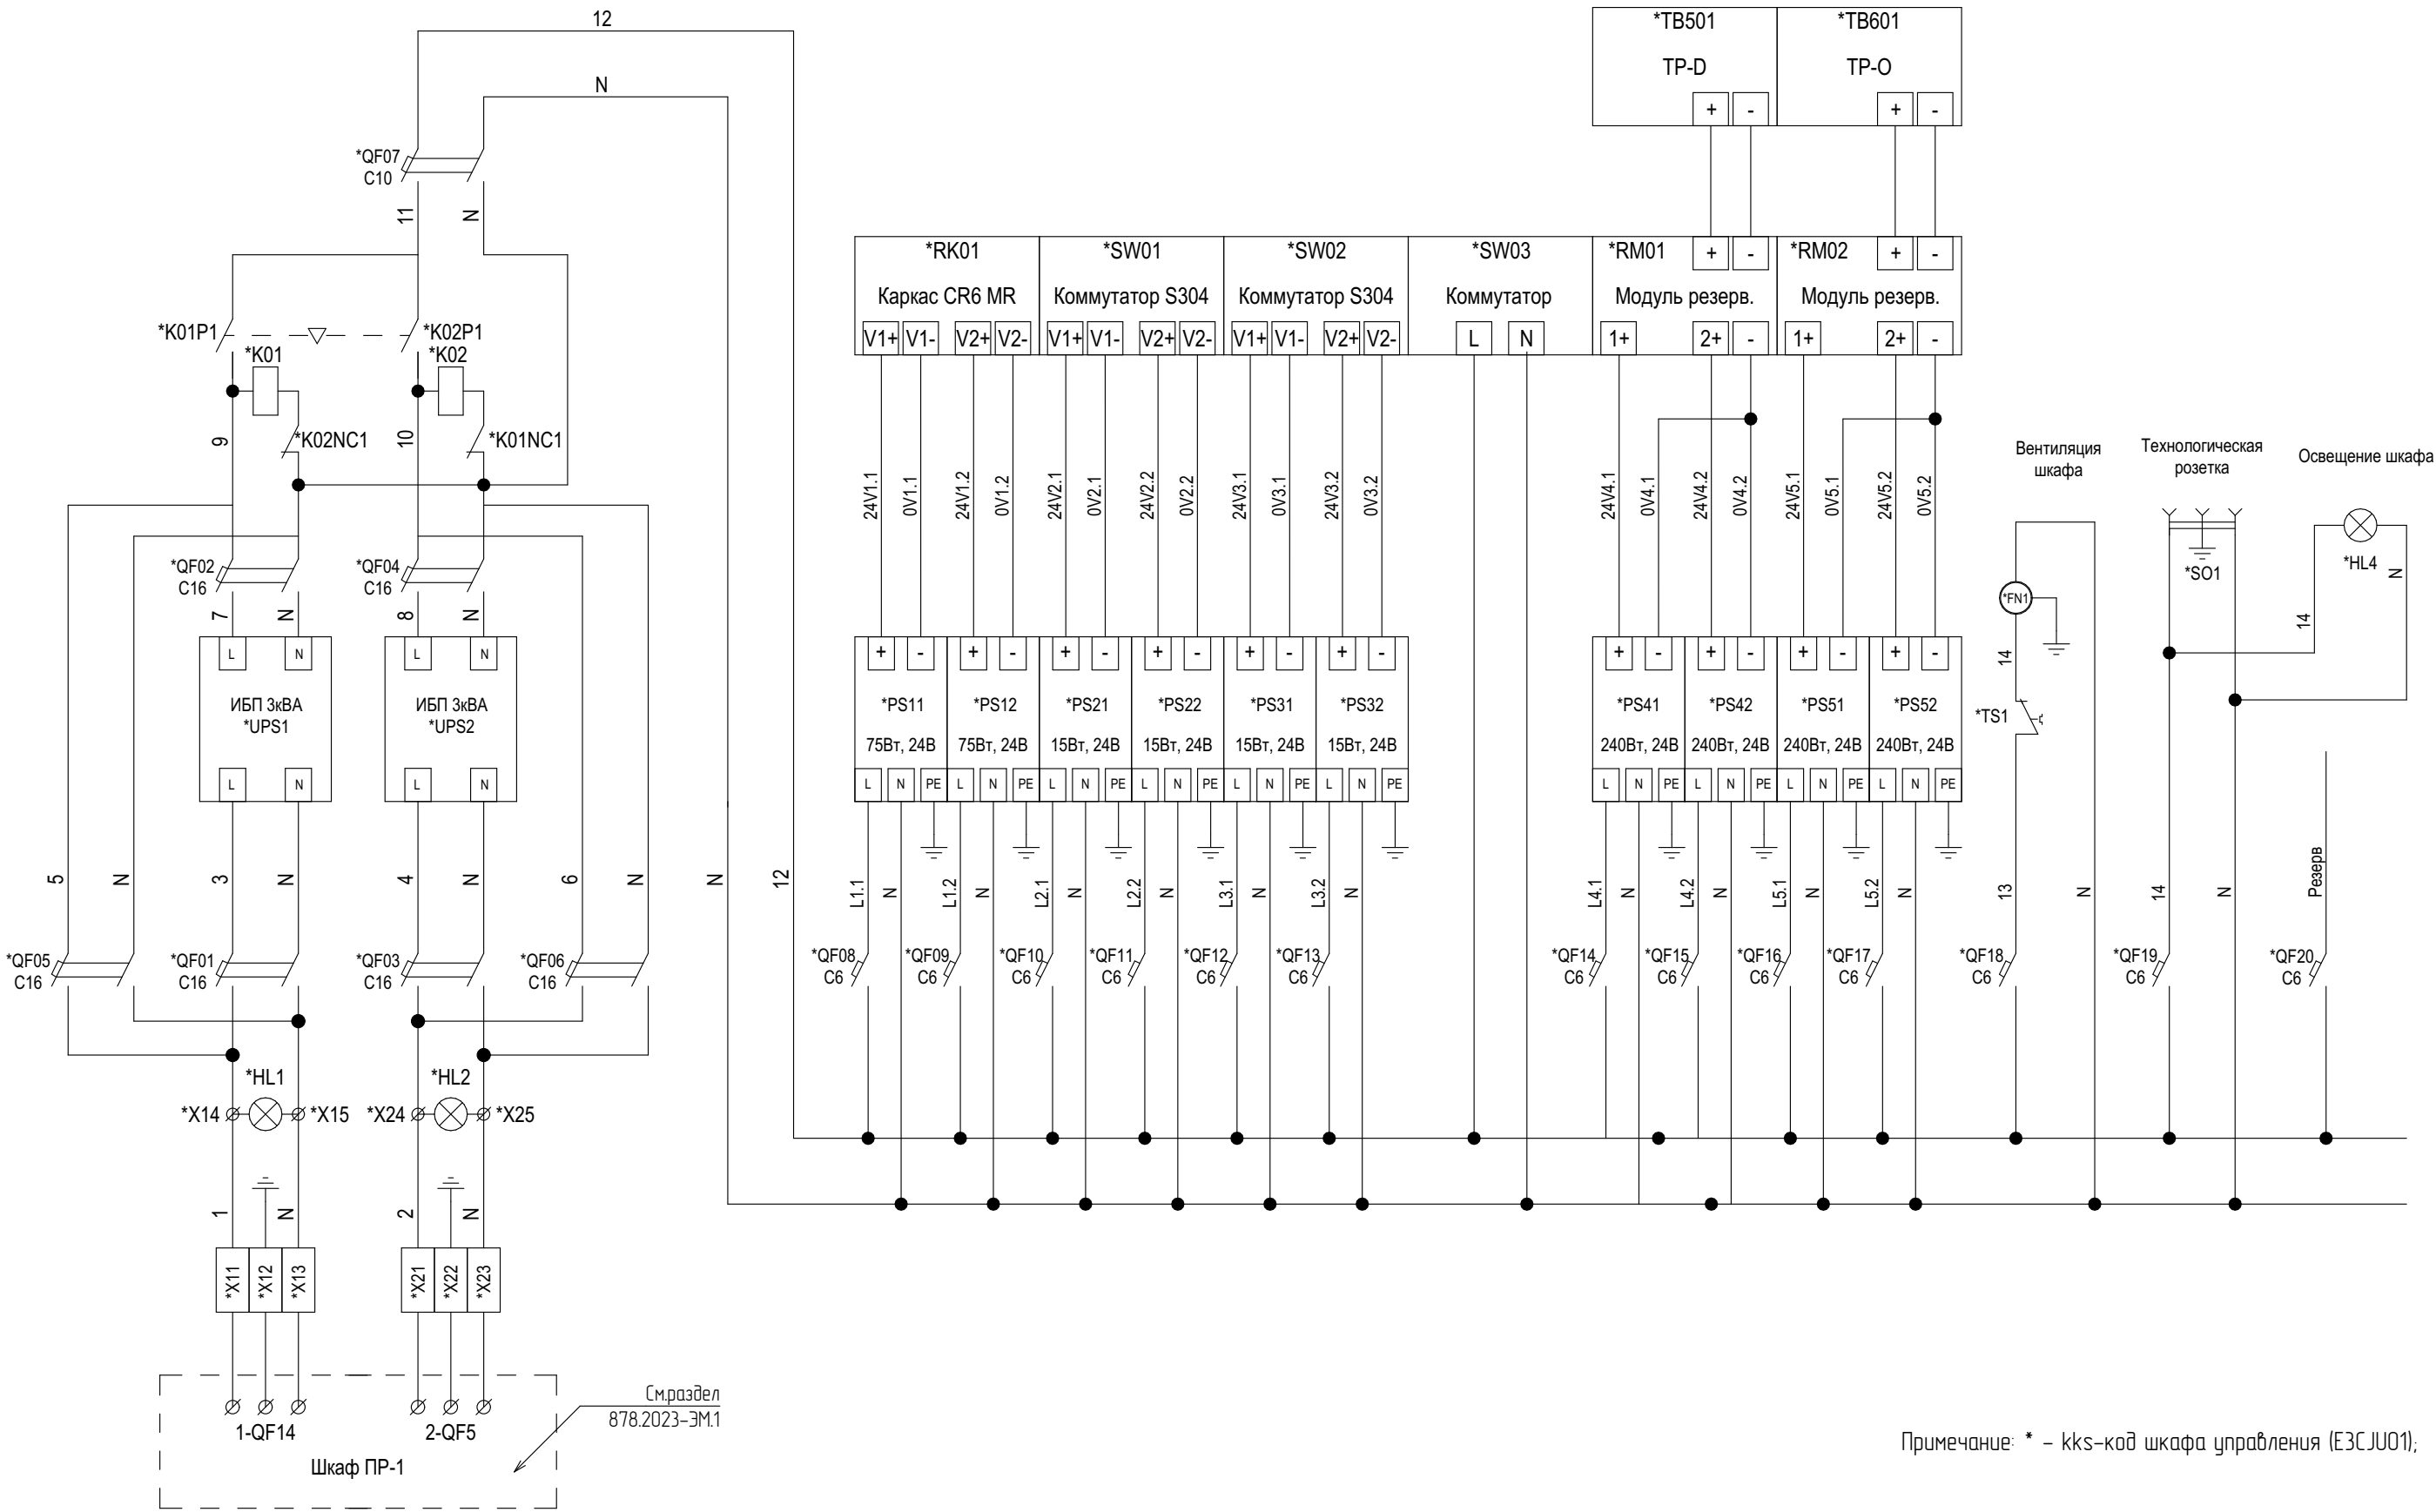


|              |              |              |              |              |
|--------------|--------------|--------------|--------------|--------------|
| Изм. № подл. | Подп. и дата | Взам. инв. № | Инв. № дубл. | Подп. и дата |
|              |              |              |              |              |

|      |      |          |       |      |                      |           |
|------|------|----------|-------|------|----------------------|-----------|
| Изм. | Лист | № докум. | Подп. | Дата | 878.2023-АСУ ТП.СБ.1 | Лист<br>9 |
|------|------|----------|-------|------|----------------------|-----------|

7 Схема серверного шкафа Z0CJU01

Принципиальная электрическая схема шкафа


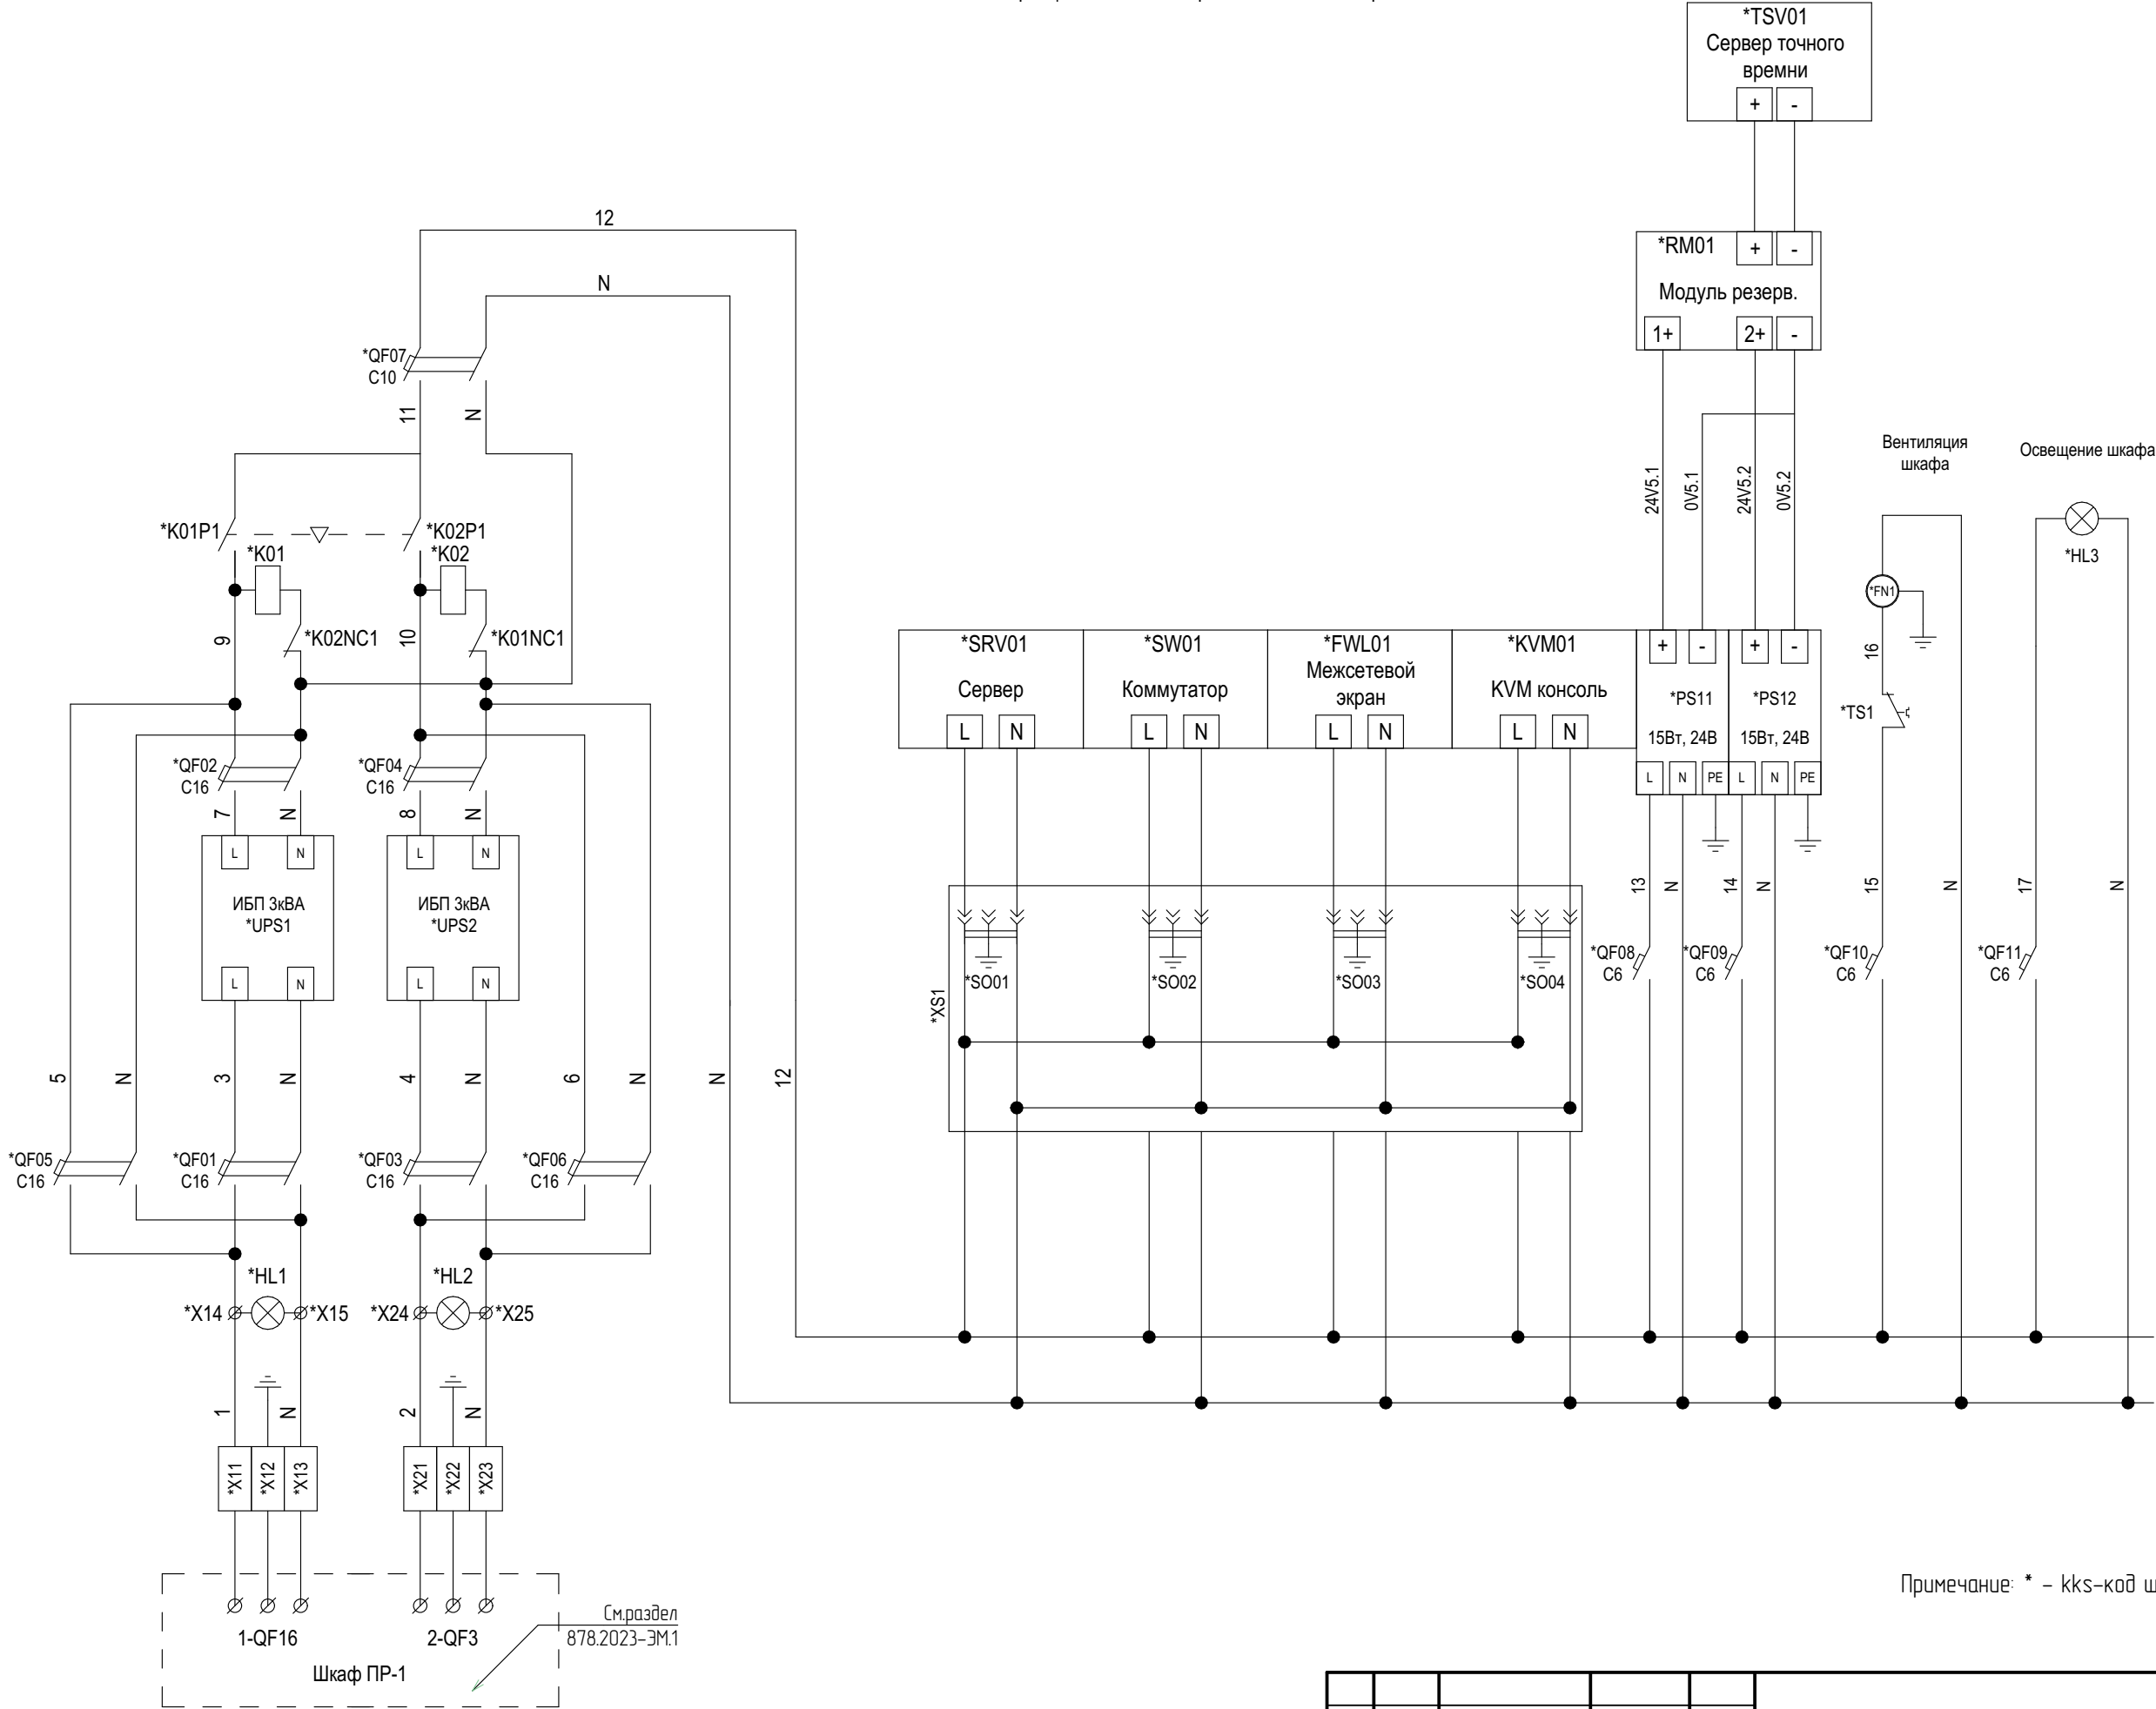


Примечание: \* - kks-код шкафа управления (Z0CJU01);

|              |              |              |              |              |
|--------------|--------------|--------------|--------------|--------------|
| Изм. № подл. | Подп. и дата | Взам. инв. № | Инв. № дубл. | Подп. и дата |
|              |              |              |              |              |

8 Схема серверного шкафа Z0CJU02

Принципиальная электрическая схема шкафа

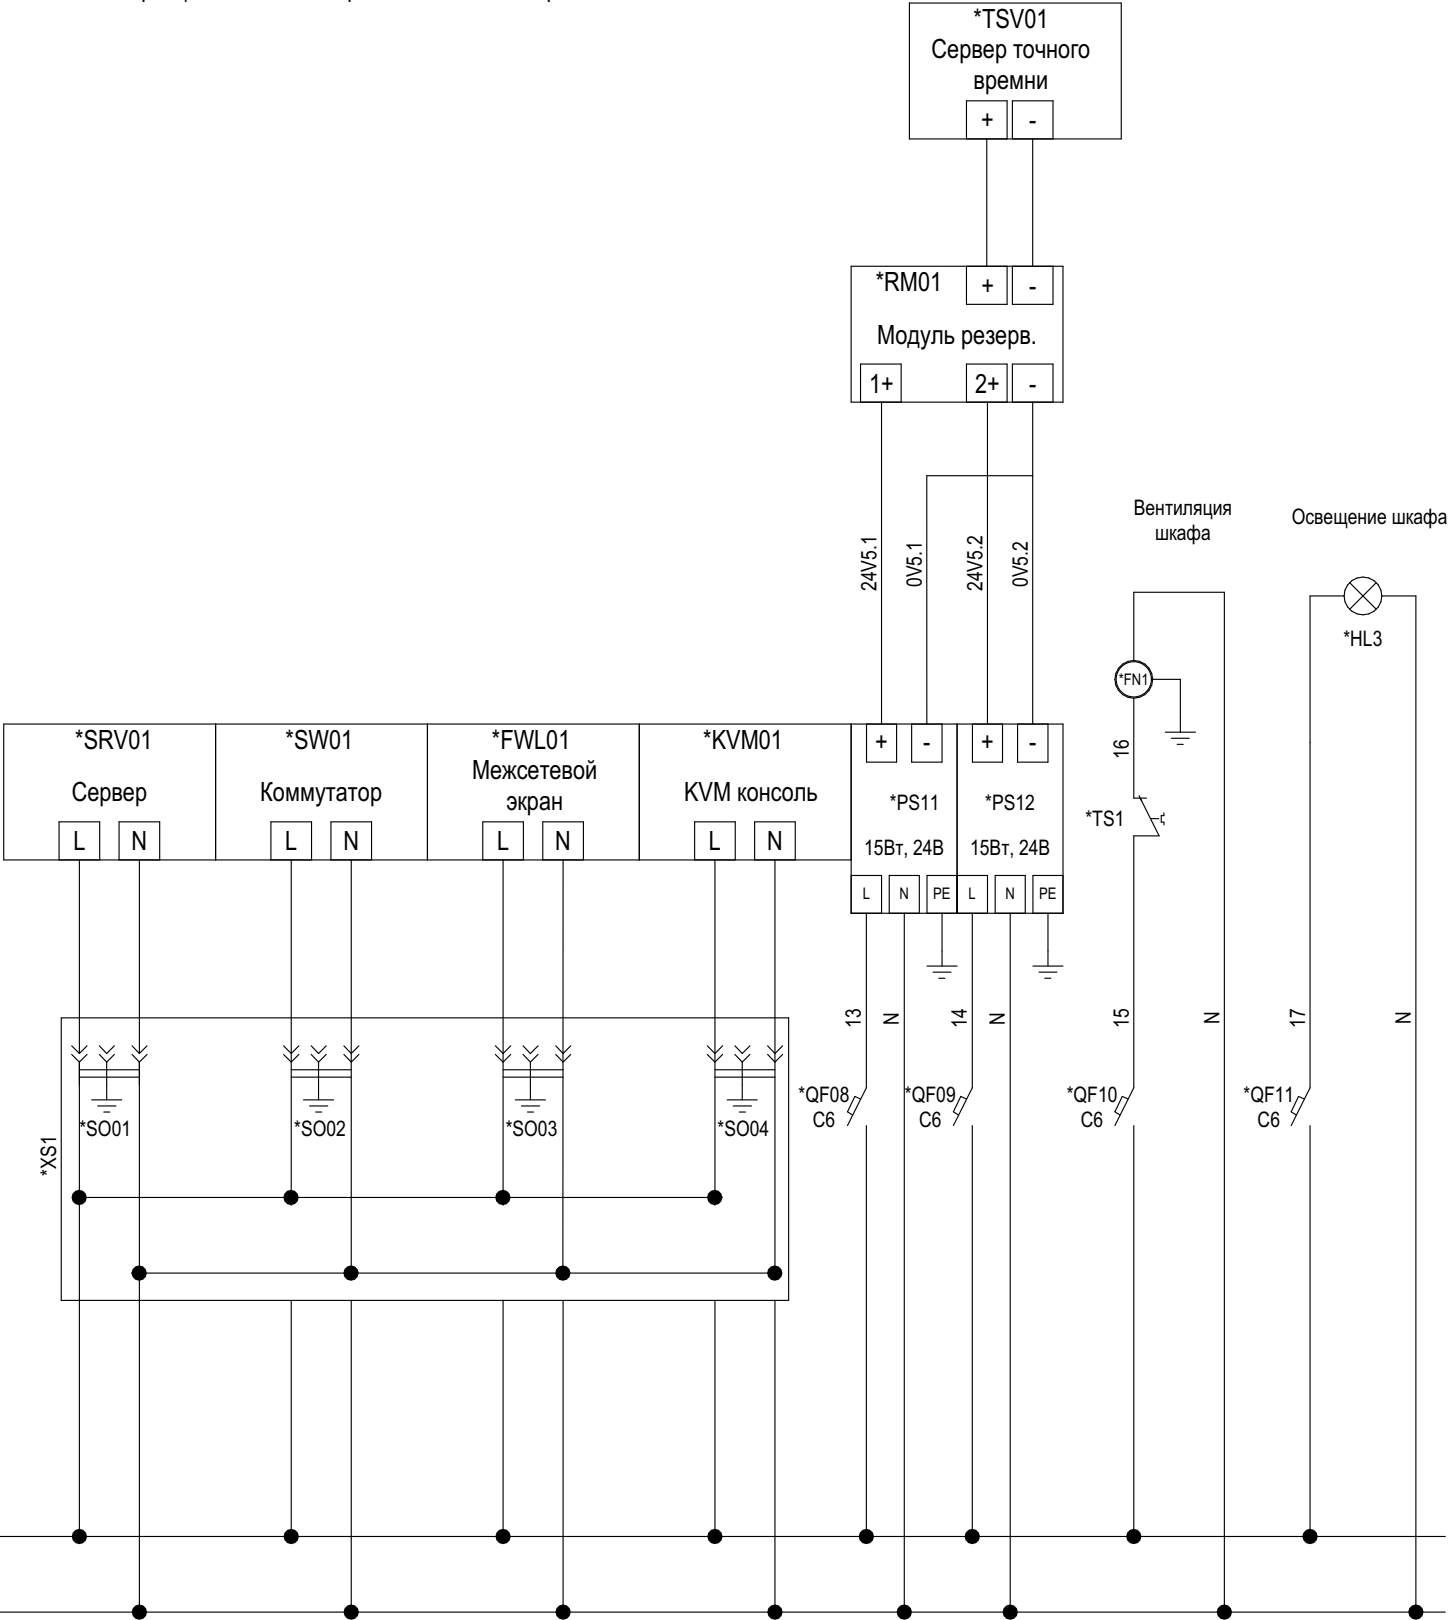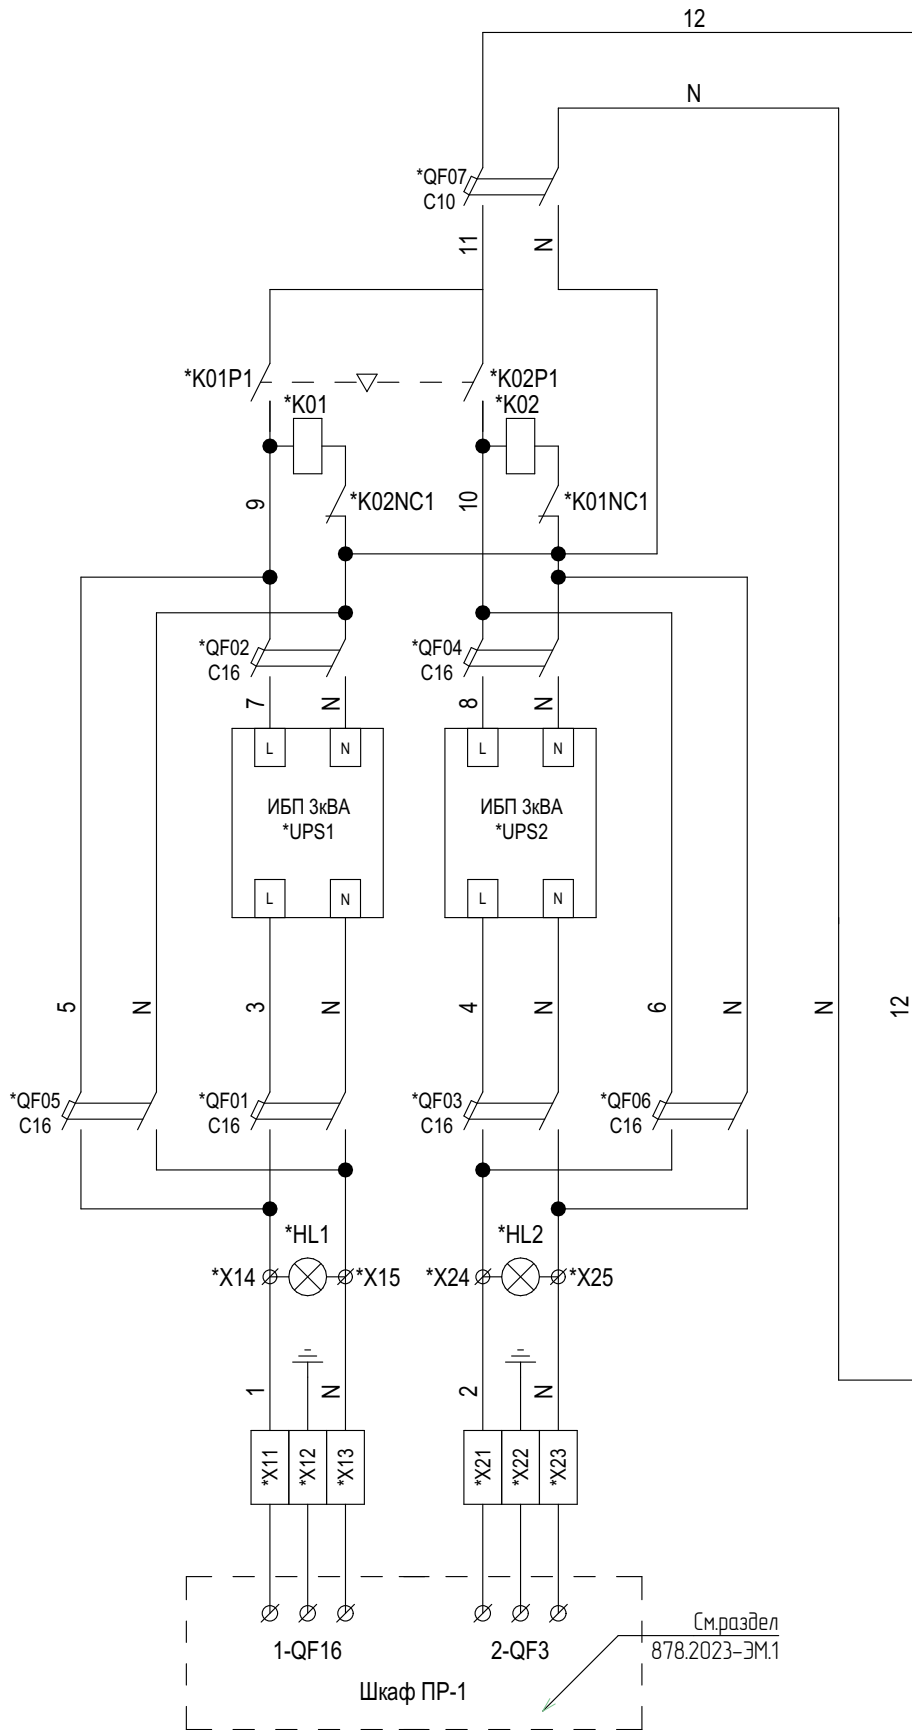

Примечание: \* - kks-код шкафа управления (Z0CJU02);

|              |              |               |              |              |
|--------------|--------------|---------------|--------------|--------------|
| Изм. № подл. | Подп. и дата | Взамен шив. № | Изм. № дубл. | Подп. и дата |
|              |              |               |              |              |

# Лист регистрации изменений

[illegible]

| Инв. № подл. | Подп. и дата | Взамен инв. № | Инв. № дубл. | Подп. и дата |
|--------------|--------------|---------------|--------------|--------------|
|              |              |               |              |              |

|      |      |          |       |      |                      |      |
|------|------|----------|-------|------|----------------------|------|
|      |      |          |       |      | 878.2023-АСУ ТП.СБ.1 | Лист |
|      |      |          |       |      |                      | 12   |
| Изм. | Лист | № докум. | Подп. | Дата |                      |      |