


3 Функциональная схема НАБ

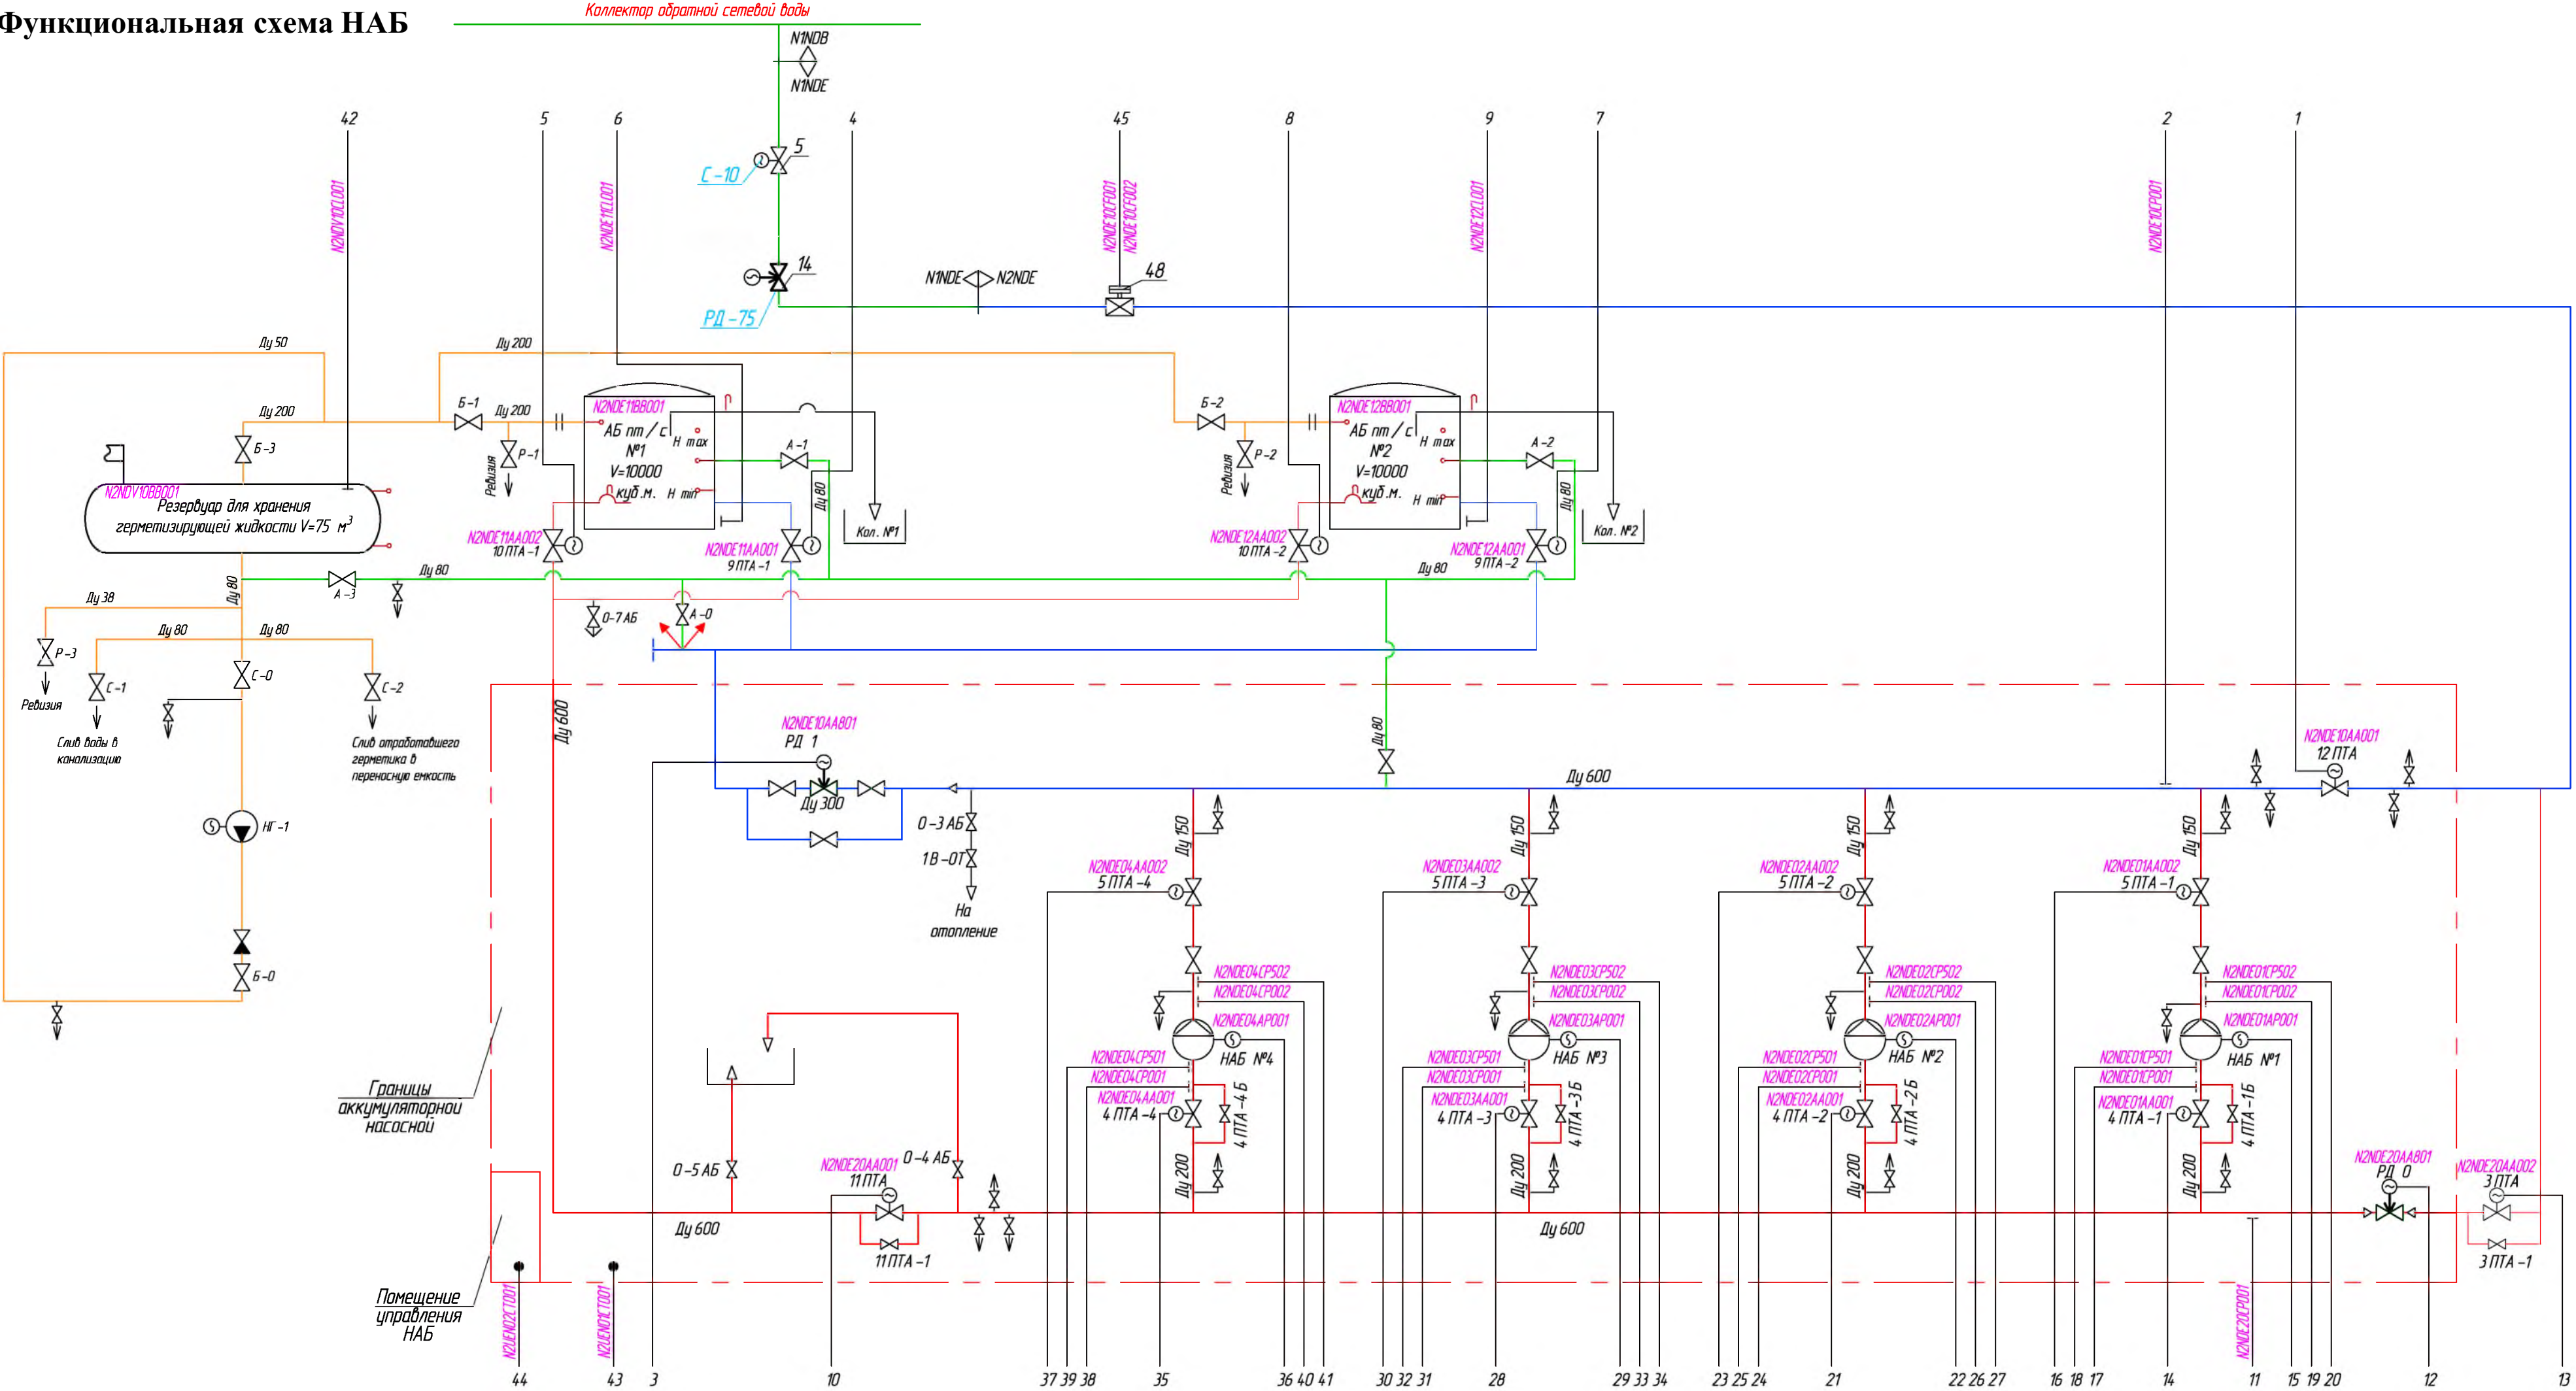

Условные обозначения:

- PI - манометр;
- PT - датчик давления;
- TT - датчик температуры;
- FT - датчик расхода;

- NS - пусковая аппаратура для управления электродвигателем;
- Запорная арматура с эл. приводом;
- Запорная арматура с эл. приводом;
- Обратный клапан.

- Трубопроводы заполнения баков
- Трубопроводы откачки из баков
- Насосы аккумуляторных баков
- Трубопроводы герметика
- Трубопроводы воды для перемещения герметика

Инв. № подл.	Подп. и дата	Взамен инв. №	Инв. № дубл.	Подп. и дата

[illegible]

					878.2023-АЧУ ТП.С2	Лист
Изм.	Лист	№ докум.	Подп.	Дата		27