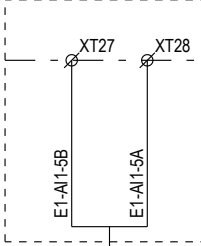
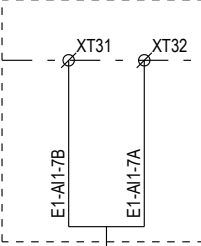
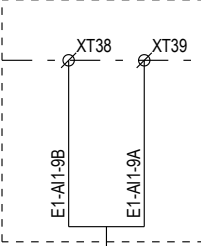
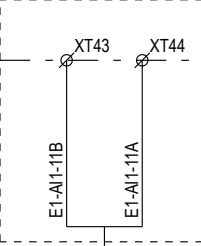
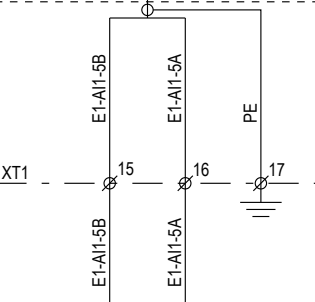
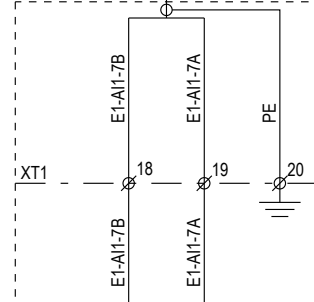
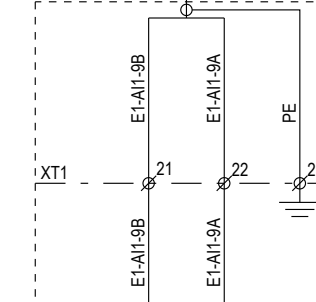
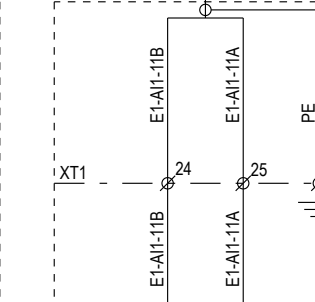
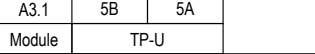
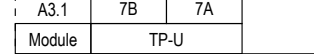
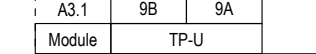
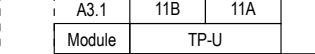


[illegible]

[illegible]





Назначение	Давление на выходе ГРП-1 (13a)	Давление на входе ГРП-1 (14a)	Давление после заслонки №1 (11a)	Давление после заслонки №2 (12a)																								
KKS	E1EKG01 CP001	E1EKA01 CP001	E1EKD01 CP001	E1EKD02 CP001																								
Клеммник шкафа	ЩА сущ. ГРП-1	ЩА сущ. ГРП-1	ЩА сущ. ГРП-1	ЩА сущ. ГРП-1																								
Маркировка жил кабеля/провода																												
Маркировка кабеля/провода	E1-6	E1-7	E1-8	E1-9																								
Марка, тип, длина кабеля	МКЭШнг(А)-LS 3x0,75	МКЭШнг(А)-LS 3x0,75	МКЭШнг(А)-LS 3x0,75	МКЭШнг(А)-LS 3x0,75																								
Маркировка жил кабеля/провода																												
Клеммник шкафа	Шкаф АСУ ГРП-1 (E1CJU01)	Шкаф АСУ ГРП-1 (E1CJU01)	Шкаф АСУ ГРП-1 (E1CJU01)	Шкаф АСУ ГРП-1 (E1CJU01)																								
Маркировка провода																												
Клеммники терминальной панели	<table><tr><td>A3.1</td><td>5B</td><td>5A</td></tr><tr><td>Module</td><td colspan="2">TP-U</td></tr></table>	A3.1	5B	5A	Module	TP-U		<table><tr><td>A3.1</td><td>7B</td><td>7A</td></tr><tr><td>Module</td><td colspan="2">TP-U</td></tr></table>	A3.1	7B	7A	Module	TP-U		<table><tr><td>A3.1</td><td>9B</td><td>9A</td></tr><tr><td>Module</td><td colspan="2">TP-U</td></tr></table>	A3.1	9B	9A	Module	TP-U		<table><tr><td>A3.1</td><td>11B</td><td>11A</td></tr><tr><td>Module</td><td colspan="2">TP-U</td></tr></table>	A3.1	11B	11A	Module	TP-U	
A3.1	5B	5A																										
Module	TP-U																											
A3.1	7B	7A																										
Module	TP-U																											
A3.1	9B	9A																										
Module	TP-U																											
A3.1	11B	11A																										
Module	TP-U																											
Модуль ввода/вывода	<table><tr><td colspan="2">CIDCS-6-3-0-3-3</td></tr><tr><td>XP1</td><td>M1234A-0</td></tr></table>	CIDCS-6-3-0-3-3		XP1	M1234A-0	
CIDCS-6-3-0-3-3																												
XP1	M1234A-0																											
CIDCS-6-3-0-3-3																												
XP1	M1234A-0																											
CIDCS-6-3-0-3-3																												
XP1	M1234A-0																											
CIDCS-6-3-0-3-3																												
XP1	M1234A-0																											

						878.2023-АСУ ТП.СБ.2			
						РФ, Ивановская область, г.Иваново, ул. Суворова, 76			
Изм.	Кол.уч.	Лист	№ док.	Подп.	Дата	Строительство водогрейной котельной 400Гкал/час на территории Ивановской ТЭЦ-2	Стадия	Лист	Листов
							РД	247	
Разработал	Чураков			07.25	Схема электрическая se0009: E1EKG01 CP001, E1EKA01 CP001, E1EKD01 CP001, E1EKD02 CP001		ООО НПП "ЭСН" www.nppesn.ru		
Проверил	Корепанов								
Н.контр.	Агафонов								

[illegible]

	Назначение			Неисправность шкафа сборки задвижек E1CDA01 GH002							
	KKS			Сборка СЗ ГРП-1 (E1CDA01GH002)							
	Клеммники шкафа										
	Маркировка жил кабеля/провода										
	Маркировка кабеля/провода			E1-29							
	Марка, тип, длина кабеля			МКЭШвнг(А)-LS 1x2x0,75							
	Маркировка жил кабеля/провода			L=							
	Клеммник шкафа			Lg=							
	Плюс датчика 24В			Lt=							
	Минус датчика 24В										
Маркировка провода											
Реле											
Маркировка провода											
Клеммники терминальной панели											
Модуль ввода/вывода											
Согласовано											
						Взамен инв. №					
						Подп. и дата					
						Инв. № подл.					

						878.2023-АСУ ТП.СБ.2						
						РФ, Ивановская область, г.Иваново, ул. Суворова, 76						
Изм.	Кол.уч.	Лист	№ док.	Подп.	Дата	Строительство водогрейной котельной 400Гкал/час на территории Ивановской ТЭЦ-2			Стадия	Лист	Листов	
									РД	249		
Разработал		Чураков				07.25		Схема электрическая se0019: E1CDA01 GH002			ООО НПП "ЭСН" www.nppesn.ru	
Проверил		Корепанов										
Н.контр.		Агафонов										

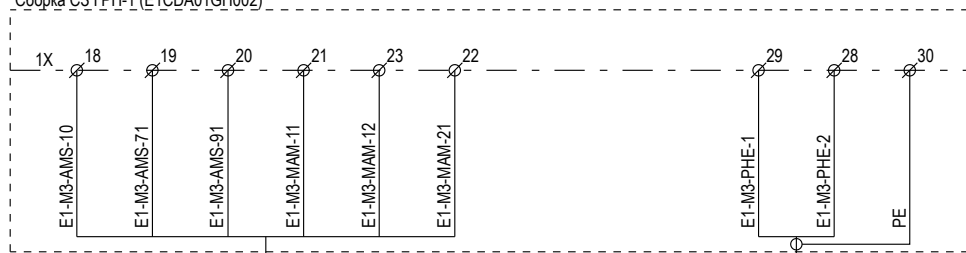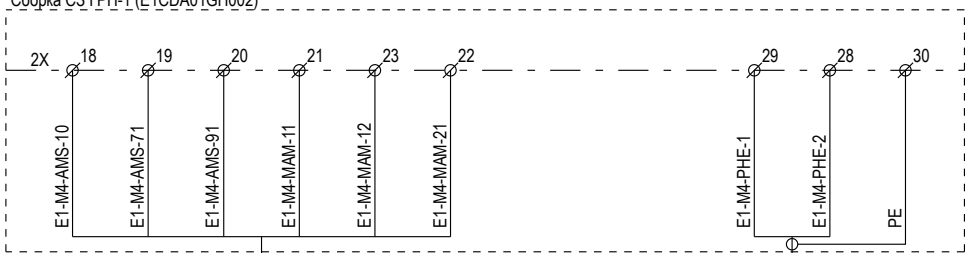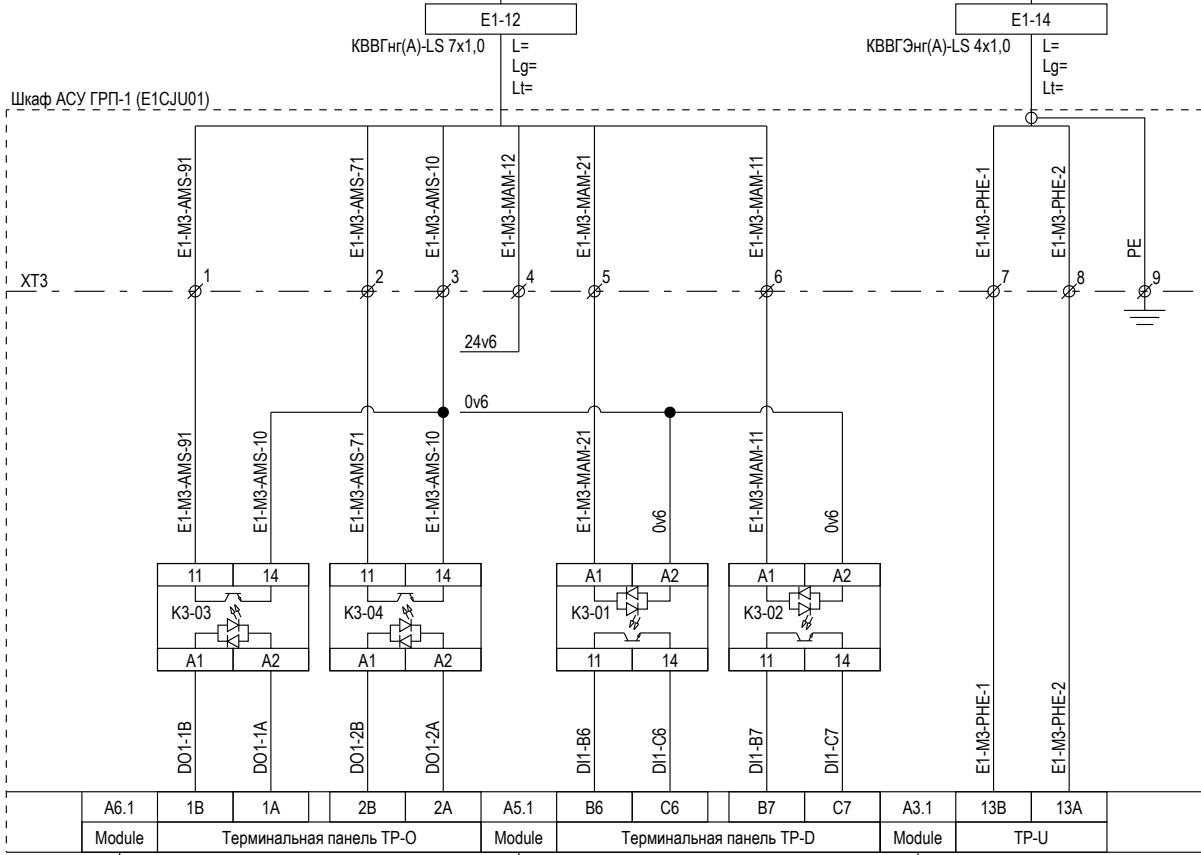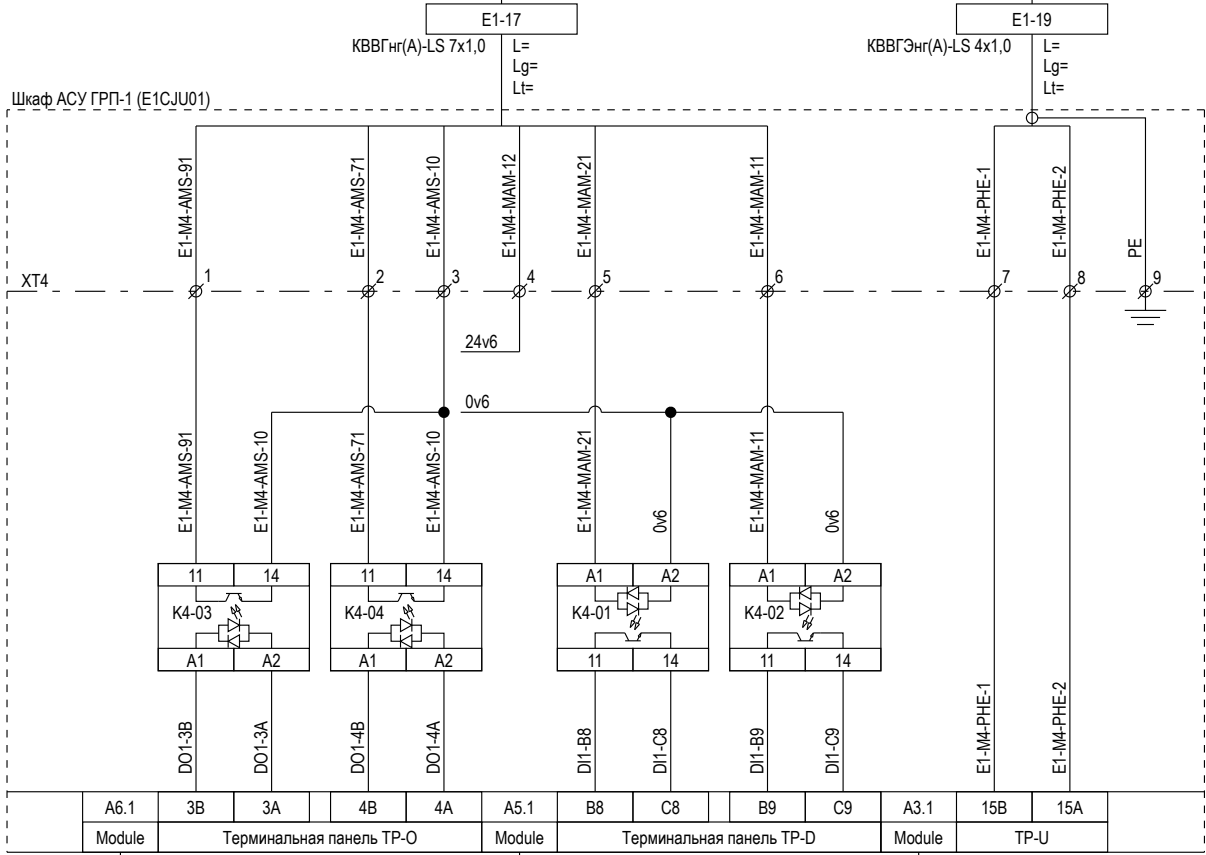	Оборудование			Регулирующая заслонка №1 E1EKD01 AA801			Регулирующая заслонка №2 E1EKD02 AA801					
	KKS			Сборка СЗ ГРП-1 (E1CDA01GH002) 			Сборка СЗ ГРП-1 (E1CDA01GH002) 					
	Клеммник шкафа			Шкаф АСУ ГРП-1 (E1CJU01) 			Шкаф АСУ ГРП-1 (E1CJU01) 					
	Маркировка жил кабеля/провода			Питание +24В			Питание +24В					
	Маркировка кабеля/провода			Ноль -24В			Ноль -24В					
	Марка, тип, длина кабеля			Маркировка провода			Маркировка провода					
	Маркировка жил кабеля/провода			Реле			Реле					
	Клеммник шкафа			Маркировка провода			Маркировка провода					
	Питание +24В			Клеммники терминальной панели			Клеммники терминальной панели					
	Ноль -24В			Описание сигнала			Описание сигнала					
Согласовано				Модуль ввода/вывода			Модуль ввода/вывода					
				CIDCS-6-3-0-3-3			CIDCS-6-3-0-3-3					
				CIDCS-6-3-0-3-3			CIDCS-6-3-0-3-3					
				CIDCS-6-3-0-3-3			CIDCS-6-3-0-3-3					
				CIDCS-6-3-0-3-3			CIDCS-6-3-0-3-3					
				CIDCS-6-3-0-3-3			CIDCS-6-3-0-3-3					
				CIDCS-6-3-0-3-3			CIDCS-6-3-0-3-3					
				CIDCS-6-3-0-3-3			CIDCS-6-3-0-3-3					
				CIDCS-6-3-0-3-3			CIDCS-6-3-0-3-3					
				CIDCS-6-3-0-3-3			CIDCS-6-3-0-3-3					
				CIDCS-6-3-0-3-3			CIDCS-6-3-0-3-3					
				CIDCS-6-3-0-3-3			CIDCS-6-3-0-3-3					
				CIDCS-6-3-0-3-3			CIDCS-6-3-0-3-3					
				CIDCS-6-3-0-3-3			CIDCS-6-3-0-3-3					
				CIDCS-6-3-0-3-3			CIDCS-6-3-0-3-3					
				CIDCS-6-3-0-3-3			CIDCS-6-3-0-3-3					
				CIDCS-6-3-0-3-3			CIDCS-6-3-0-3-3					
				CIDCS-6-3-0-3-3			CIDCS-6-3-0-3-3					
				CIDCS-6-3-0-3-3			CIDCS-6-3-0-3-3					
				CIDCS-6-3-0-3-3			CIDCS-6-3-0-3-3					
				CIDCS-6-3-0-3-3			CIDCS-6-3-0-3-3					
				CIDCS-6-3-0-3-3			CIDCS-6-3-0-3-3					
				CIDCS-6-3-0-3-3			CIDCS-6-3-0-3-3					
				CIDCS-6-3-0-3-3			CIDCS-6-3-0-3-3					
				CIDCS-6-3-0-3-3			CIDCS-6-3-0-3-3					
				CIDCS-6-3-0-3-3			CIDCS-6-3-0-3-3					
				CIDCS-6-3-0-3-3			CIDCS-6-3-0-3-3					
				CIDCS-6-3-0-3-3			CIDCS-6-3-0-3-3					
				CIDCS-6-3-0-3-3			CIDCS-6-3-0-3-3					
				CIDCS-6-3-0-3-3			CIDCS-6-3-0-3-3					
				CIDCS-6-3-0-3-3			CIDCS-6-3-0-3-3					
				CIDCS-6-3-0-3-3			CIDCS-6-3-0-3-3					
				CIDCS-6-3-0-3-3			CIDCS-6-3-0-3-3					
				CIDCS-6-3-0-3-3			CIDCS-6-3-0-3-3					
				CIDCS-6-3-0-3-3			CIDCS-6-3-0-3-3					
				CIDCS-6-3-0-3-3			CIDCS-6-3-0-3-3					
				CIDCS-6-3-0-3-3			CIDCS-6-3-0-3-3					
				CIDCS-6-3-0-3-3			CIDCS-6-3-0-3-3					
				CIDCS-6-3-0-3-3			CIDCS-6-3-0-3-3					
				CIDCS-6-3-0-3-3			CIDCS-6-3-0-3-3					
				CIDCS-6-3-0-3-3			CIDCS-6-3-0-3-3					
				CIDCS-6-3-0-3-3			CIDCS-6-3-0-3-3					
				CIDCS-6-3-0-3-3			CIDCS-6-3-0-3-3					
				CIDCS-6-3-0-3-3			CIDCS-6-3-0-3-3					
				CIDCS-6-3-0-3-3			CIDCS-6-3-0-3-3					
				CIDCS-6-3-0-3-3			CIDCS-6-3-0-3-3					
				CIDCS-6-3-0-3-3			CIDCS-6-3-0-3-3					
				CIDCS-6-3-0-3-3			CIDCS-6-3-0-3-3					
				CIDCS-6-3-0-3-3			CIDCS-6-3-0-3-3					
				CIDCS-6-3-0-3-3			CIDCS-6-3-0-3-3					
				CIDCS-6-3-0-3-3			CIDCS-6-3-0-3-3					
				CIDCS-6-3-0-3-3			CIDCS-6-3-0-3-3					
				CIDCS-6-3-0-3-3			CIDCS-6-3-0-3-3					
				CIDCS-6-3-0-3-3			CIDCS-6-3-0-3-3					
				CIDCS-6-3-0-3-3			CIDCS-6-3-0-3-3					
				CIDCS-6-3-0-3-3			CIDCS-6-3-0-3-3					
				CIDCS-6-3-0-3-3			CIDCS-6-3-0-3-3					
				CIDCS-6-3-0-3-3			CIDCS-6-3-0-3-3					
				CIDCS-6-3-0-3-3			CIDCS-6-3-0-3-3					
				CIDCS-6-3-0-3-3			CIDCS-6-3-0-3-3					
				CIDCS-6-3-0-3-3			CIDCS-6-3-0-3-3					
				CIDCS-6-3-0-3-3			CIDCS-6-3-0-3-3					
				CIDCS-6-3-0-3-3			CIDCS-6-3-0-3-3					
				CIDCS-6-3-0-3-3			CIDCS-6-3-0-3-3					
				CIDCS-6-3-0-3-3			CIDCS-6-3-0-3-3					
				CIDCS-6-3-0-3-3			CIDCS-6-3-0-3-3					
				CIDCS-6-3-0-3-3			CIDCS-6-3-0-3-3					
				CIDCS-6-3-0-3-3			CIDCS-6-3-0-3-3					
				CIDCS-6-3-0-3-3			CIDCS-6-3-0-3-3					
				CIDCS-6-3-0-3-3			CIDCS-6-3-0-3-3					
				CIDCS-6-3-0-3-3			CIDCS-6-3-0-3-3					
				CIDCS-6-3-0-3-3			CIDCS-6-3-0-3-3					
				CIDCS-6-3-0-3-3			CIDCS-6-3-0-3-3					
				CIDCS-6-3-0-3-3			CIDCS-6-3-0-3-3					
				CIDCS-6-3-0-3-3			CIDCS-6-3-0-3-3					
				CIDCS-6-3-0-3-3			CIDCS-6-3-0-3-3					
				CIDCS-6-3-0-3-3			CIDCS-6-3-0-3-3					
				CIDCS-6-3-0-3-3			CIDCS-6-3-0-3-3					
				CIDCS-6-3-0-3-3			CIDCS-6-3-0-3-3					
				CIDCS-6-3-0-3-3			CIDCS-6-3-0-3-3					
				CIDCS-6-3-0-3-3			CIDCS-6-3-0-3-3					
				CIDCS-6-3-0-3-3			CIDCS-6-3-0-3-3					
				CIDCS-6-3-0-3-3			CIDCS-6-3-0-3-3					
				CIDCS-6-3-0-3-3			CIDCS-6-3-0-3-3					
				CIDCS-6-3-0-3-3			CIDCS-6-3-0-3-3					
				CIDCS-6-3-0-3-3			CIDCS-6-3-0-3-3					
				CIDCS-6-3-0-3-3			CIDCS-6-3-0-3-3					
				CIDCS-6-3-0-3-3			CIDCS-6-3-0-3-3					
				CIDCS-6-3-0-3-3			CIDCS-6-3-0-3-3					
				CIDCS-6-3-0-3-3			CIDCS-6-3-0-3-3					
				CIDCS-6-3-0-3-3			CIDCS-6-3-0-3-3					
				CIDCS-6-3-0-3-3			CIDCS-6-3-0-3-3					
				CIDCS-6-3-0-3-3			CIDCS-6-3-0-3-3					
				CIDCS-6-3-0-3-3			CIDCS-6-3-0-3-3					
				CIDCS-6-3-0-3-3			CIDCS-6-3-0-3-3					
				CIDCS-6-3-0-3-3			CIDCS-6-3-0-3-3					
				CIDCS-6-3-0-3-3			CIDCS-6-3-0-3-3					
				CIDCS-6-3-0-3-3			CIDCS-6-3-0-3-3					
				CIDCS-6-3-0-3-3			CIDCS-6-3-0-3-3					
				CIDCS-6-3-0-3-3								

Оборудование

KKS

Клеммник шкафа

Маркировка жил кабеля/провода

Маркировка кабеля/провода

Марка, тип, длина кабеля

Маркировка жил кабеля/провода

Клеммник шкафа

Маркировка провода

Реле

Маркировка провода

Клеммники терминальной панели

Описание сигнала

Модуль ввода/вывода

Дисковый затвор ГК-1
E1EKG12 AA001

Сборка СЗ ГРП-1 (E1CDA01GH002)

5х1

2

5

7

8

11

14

18

19

20

21

25

E1-M7-A1

E1-M7-A5

E1-M7-A11

E1-M7-A12

E1-M7-A30

E1-M7-A19

E1-M7-A20

E1-M7-A6

E1-M7-A7

E1-M7-A8

E1-M7-A9

E1-M7-H1

E1-27

KBBГнг(A)-LS 19х1.0 (7р)

L=

Lg=

L=

Шкаф АСУ ГРП-1 (E1CJU01)

ХТ7

1

2

3

4

5

6

7

8

9

10

11

12

E1-M7-A1

E1-M7-A5

E1-M7-A11

E1-M7-A12

E1-M7-A19

E1-M7-A20

E1-M7-A9

E1-M7-A8

E1-M7-A6

E1-M7-A30

E1-M7-A7

E1-M7-H1

11

12

11

14

11

14

A1

A2

11

14

A1

A2

11

14

A1

A2

11

14

A1

A2

K7-10

K7-03

K7-04

K7-01

K7-02

K7-06

K7-07

K7-05

A1

A2

A1

A2

A1

A2

A1

A2

A1

A2

A1

A2

A1

A2

A1

A2

DO1-11B

DO1-11A

DO1-12B

DO1-12A

DO1-13B

DO1-13A

DI1-B18

DI1-C18

DI1-B19

DI1-C19

DI1-B20

DI1-C20

DI1-B21

DI1-C21

DI1-B22

DI1-C22

A6.1

11B

11A

12B

12A

13B

13A

A5.1

B18

C18

B19

C19

B20

C20

B21

C21

B22

C22

Module

Терминальная панель TP-O

Module

Терминальная панель TP-D

Стоп

Открыт

Закреть

Открыт

Закреть

Готовность

Дистанционный режим работы

Превышение момента

CIDC-6-3-0-3-3

CIDC-6-3-0-3-3

XP1

M12510-0

XP1

M1252D-0

Согласовано

Взамен инв. №

Подп. и дата

Инв. № подл.

878.2023-АСУ ТП.СБ.2

РФ, Ивановская область, г.Иваново, ул. Суворова, 76

Изм.

Кол.уч.

Лист

№ док.

Подп.

Дата

Строительство водогрейной котельной 400Гкал/час на территории Ивановской ТЭЦ-2

РД

252

Разработал

Чураков

Проверил

Корепанов

Н.контр.

Агафонов


07.25

Схема электрическая se0028: E1EKG12 AA001

ООО НПП "ЭСН"
www.nppesn.ru

Согласовано				
Инва. № подл.	Взамен инв. №			
	Подп. и дата			


Назначение
KKS
Клеммники шкафа
Маркировка жил кабеля/провода
Маркировка кабеля/провода
Марка, тип, длина кабеля
Маркировка жил кабеля/провода
Клеммник шкафа
Плюс 24В
Минус 24В
Маркировка провода
Клеммник модуля ввода/вывода

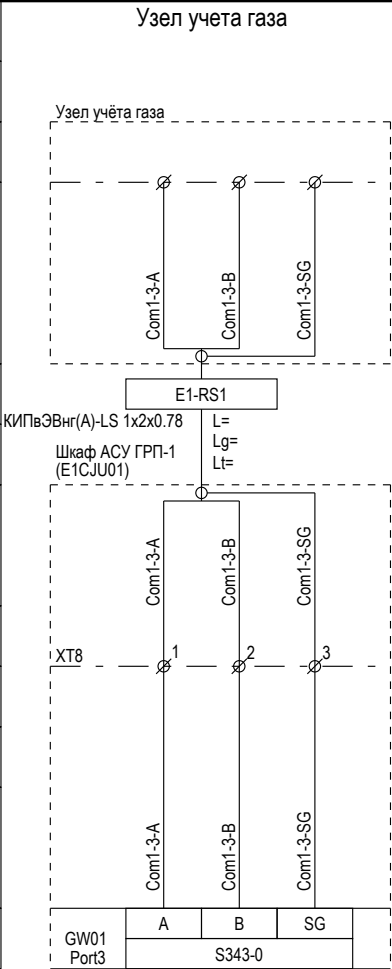

						878.2023-АСУ ТП.СБ.2			
						РФ, Ивановская область, г.Иваново, ул. Суворова, 76			
Изм.	Кол.уч.	Лист	№ док.	Подп.	Дата	Строительство водогрейной котельной 400Гкал/час на территории Ивановской ТЭЦ-2	Стадия	Лист	Листов
							РД	253	
Разработал	Чураков				07.25	Схема электрическая se0020:	ООО НПП "ЭСН" www.nppesn.ru		
Проверил	Корепанов								
Н.контр.	Агафонов								

Согласовано			
Инва. № подл.	Подп. и дата	Взамен инв. №	

Назначение
KKS
Тип прибора
Контакт прибора
Маркировка жил кабеля/провода
Плюс датчика 24В
Минус датчика 24В
Маркировка провода
Реле
Маркировка провода
Клеммники терминальной панели
Модуль ввода/вывода

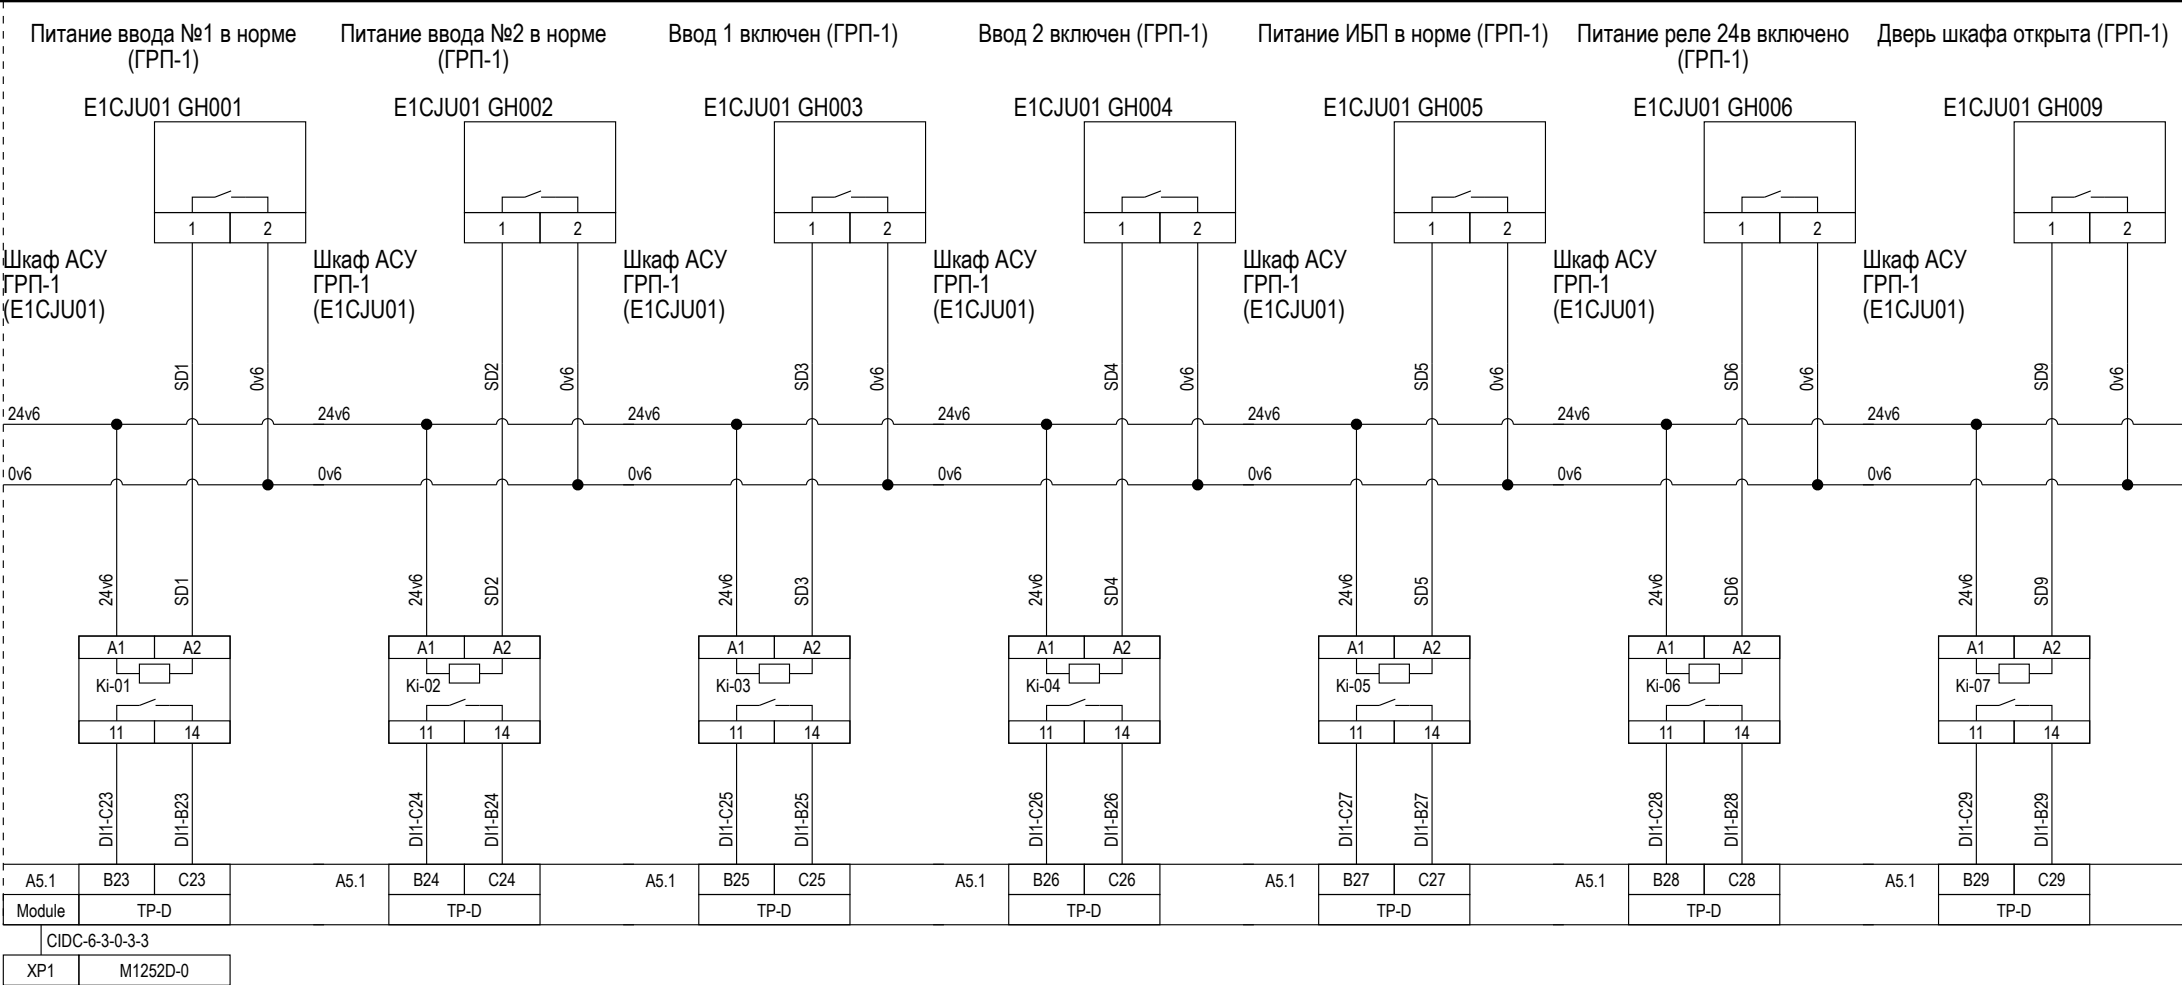

						878.2023-АСУ ТП.СБ.2		
						РФ, Ивановская область, г.Иваново, ул. Суворова, 76		
Изм.	Кол.уч.	Лист	№ док.	Подп.	Дата	Строительство водогрейной котельной 400Гкал/час на территории Ивановской ТЭЦ-2	Стадия	Лист
							РД	254
Разработал	Чураков				07.25	Схема электрическая se0023: E1CJU01 GH001, E1CJU01 GH002, E1CJU01 GH003, E1CJU01 GH004, E1CJU01 GH005, E1CJU01 GH006, E1CJU01 GH009	ООО НПП "ЭСН" www.nppesn.ru	
Проверил	Корепанов							
Н.контр.	Агафонов							