

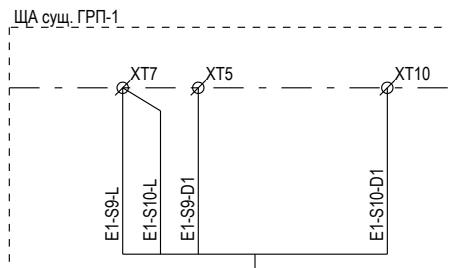
Согласовано					Шифр	Назначение	Значение номиналь-ное	Единица изме-рения	Схема электри-ческая	Схема монтажа		Шифр	Назначение	Значение номиналь-ное	Единица изме-рения	Схема электри-ческая	Схема монтажа
					E1EKE10 CP001	Давление до фильтра №1			se0005, л.244								
					E1EKE10 CP002	Давление после фильтра №1			se0005, л.244								
					E1EKE01 CP151	Засорение фильтра №1			se0024, л.245								
					E1EKG01 CT101	Температура на выходе ГРП-1 (15а)			se0007, л.246								
					E1EKA01 CT101	Температура на входе ГРП-1 (16а)			se0007, л.246								
					E1EKG01 CP001	Давление на выходе ГРП-1 (13а)			se0009, л.247								
					E1EKA01 CP001	Давление на входе ГРП-1 (14а)			se0009, л.247								
					E1EKD01 CP001	Давление после заслонки №1 (11а)			se0009, л.247								
					E1EKD02 CP001	Давление после заслонки №2 (12а)			se0009, л.247								
					E1UEN01 CQ001	Сигнализатор газов СТМ-10			se0025, л.248								
					E1CDA01 GH002	Неисправность шкафа сборки задвижек			se0019, л.249								
					E1EKD01 AA801	Регулирующая заслонка №1			se0026, л.250								
					E1EKD02 AA801	Регулирующая заслонка №2			se0026, л.250								
	Взамен инв. №					E1EKA01 AA001	Задвижка 2-Г			se0027, л.251							
					E1EKG11 AA001	Задвижка 3-Г			se0027, л.251								
					E1EKG12 AA001	Дисковый затвор ГК-1			se0028, л.252								
						Узел учета газа			se0020, л.253								
					E1CJU01 GH001	Питание ввода №1 в норме (ГРП-1)			se0023, л.254								
					E1CJU01 GH002	Питание ввода №2 в норме (ГРП-1)			se0023, л.254								
					E1CJU01 GH003	Ввод 1 включен (ГРП-1)			se0023, л.254								
					E1CJU01 GH004	Ввод 2 включен (ГРП-1)			se0023, л.254								
					E1CJU01 GH005	Питание ИБП в норме (ГРП-1)			se0023, л.254								
					E1CJU01 GH006	Питание реле 24в включено (ГРП-1)			se0023, л.254								
					E1CJU01 GH009	Дверь шкафа открыта (ГРП-1)			se0023, л.254								

						878.2023-АСУ ТП.СБ.2					
						РФ, Ивановская область, г.Иваново, ул. Суворова, 76					
Изм.	Кол.уч.	Лист	№ док.	Подп.	Дата	Строительство водогрейной котельной 400Гкал/час на территории Ивановской ТЭЦ-2			Стадия	Лист	Листов
									РД	243	
Разработал	Чураков				07.25	Ведомость элементов функциональной схемы (1/1)			ООО НПП "ЭСН" www.nppesn.ru		
Проверил	Корепанов										
Н.контр.	Агафонов										

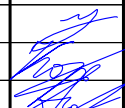
[illegible]

Назначение	Давление до фильтра №1	Давление после фильтра №1
KKS		
Тип прибора	E1EKE10CP001 AIP-20/M2-H	E1EKE10CP002 AIP-20/M2-H
Контакт прибора	1 2	1 2
Маркировка жил кабеля/провода	E1-A11-2B E1-A11-1B PE	E1-A11-4B E1-A11-3B PE
Маркировка кабеля/провода	E1-1	E1-2
Марка, тип, длина кабеля	КВВГЭнг(А)-LS 4x1,0 Шкаф АСУ ГРП-1 (E1CJU01)	КВВГЭнг(А)-LS 4x1,0 Шкаф АСУ ГРП-1 (E1CJU01)
Маркировка жил кабеля/провода	E1-A11-2B E1-A11-1B PE	E1-A11-4B E1-A11-3B PE
Клеммник шкафа	1 2 3	4 5 6
Маркировка провода	E1-A11-2B E1-A11-1B	E1-A11-4B E1-A11-3B
Клеммники терминальной панели	A3.1 2B 1B	A3.1 4B 3B
Модуль ввода/вывода	Module TP-U CIDCS-6-3-0-3-3 XP1 M1234A-0	Module TP-U CIDCS-6-3-0-3-3 XP1 M1234A-0

						878.2023-АСУ ТП.СБ.2				
						РФ, Ивановская область, г.Иваново, ул. Суворова, 76				
Изм.	Кол.уч.	Лист	№ док.	Подп.	Дата					
						Строительство водогрейной котельной 400Гкал/час на территории Ивановской ТЭЦ-2		Стадия	Лист	Листов
								РД	244	
Разработал	Чураков				07.25	Схема электрическая se0005: E1EKE10CP001, E1EKE10CP002		ООО НПП "ЭСН" www.nppesn.ru		
Проверил	Корепанов									
Н.контр.	Агафонов									

Назначение	Засорение фильтра №1		Засорение фильтра №2	
	E1EKE01CP151		E1EKE02CP151	
				
	Маркировка жил кабеля/провода			
	Маркировка кабеля/провода			
	Марка, тип, длина кабеля			
	Маркировка жил кабеля/провода			
	Клеммник шкафа			
	Реле			
	Маркировка провода			
Клеммники терминальной панели				
Модуль ввода/вывода				

Согласовано				
Взамен инв. №				
Подп. и дата				
Инв. № подл.				

878.2023-АСУ ТП.СБ.2					
РФ, Ивановская область, г.Иваново, ул. Суворова, 76					
Изм.	Кол.уч.	Лист	№ док.	Подп.	Дата
Строительство водогрейной котельной 400Гкал/час на территории Ивановской ТЭЦ-2				Стадия	Лист
				РД	245
Разработал		Чураков			07.25
Проверил		Корепанов			
Н.контр.		Агафонов			

ООО НПП "ЭСН"		
www.nppesn.ru		

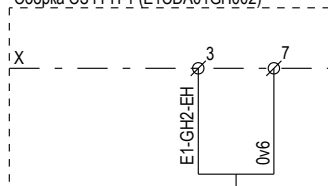
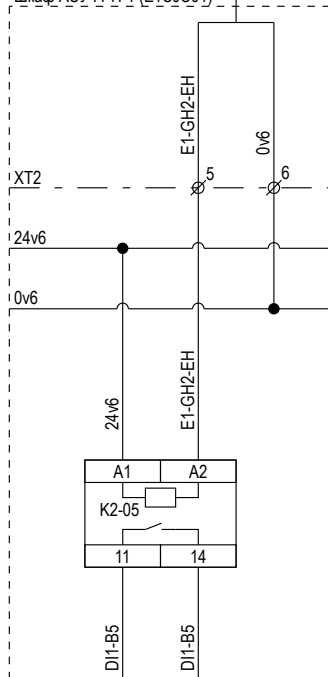
Согласовано Изм. № инв. № Подп. и дата Изм. № подл.			Назначение	Температура на выходе ГРП-1 (15а)										Температура на входе ГРП-1 (16а)	
			KKS	
			Тип прибора	
			Контакт прибора	
			Маркировка жил кабеля/провода	
			Маркировка кабеля/провода	
			Марка, тип, длина кабеля	
			Маркировка жил кабеля/провода	
			Клеммник шкафа	
			Плюс 24В	
Минус 24В	
Маркировка провода	
Клеммники терминальной панели	
Модуль ввода/вывода	
Е1ЕКГ01СТ101 4-х пров R 1 3 2 4 Е1-А12-2В Е1-А12-3В Е1-А12-1В Е1-А12-2В Е1-4 КВВГЭнг(А)-LS 4х1,0 L= Lg= Lt= Шкаф АСУ ГРП-1 (Е1СЈU01) XT1 7 8 9 10 Е1-А12-2В Е1-А12-1В Е1-А12-3В Е1-А12-2В А3.2 2В 1В 3В 2В Module TP-U CIDCS-6-3-0-3-3 XP1 M1231TR-0 Е1ЕКА01СТ101 4-х пров R 1 3 2 4 Е1-А12-4В Е1-А12-5В Е1-А12-3В Е1-А12-4В Е1-5 КВВГЭнг(А)-LS 4х1,0 L= Lg= Lt= Шкаф АСУ ГРП-1 (Е1СЈU01) XT1 11 12 13 14 Е1-А12-4В Е1-А12-3В Е1-А12-5В Е1-А12-4В А3.2 4В 3В 5В 4В Module TP-U CIDCS-6-3-0-3-3 XP1 M1231TR-0	
878.2023-АСУ ТП.СБ.2 РФ, Ивановская область, г.Иваново, ул. Суворова, 76 <table><tr><td>Изм.</td><td>Кол.уч.</td><td>Лист</td><td>№ док.</td><td>Подп.</td><td>Дата</td><td rowspan="3">Строительство водогрейной котельной 400Гкал/час на территории Ивановской ТЭЦ-2</td><td>Стадия</td><td>Лист</td><td>Листов</td></tr><tr><td></td><td></td><td></td><td></td><td></td><td></td><td>РД</td><td>246</td><td></td></tr><tr><td>Разработал</td><td>Чураков</td><td></td><td></td><td></td><td>07.25</td><td rowspan="3">Схема электрическая se0007: Е1ЕКГ01СТ101, Е1ЕКА01СТ101</td><td colspan="3" rowspan="3">ООО НПП "ЭСН" www.nppesn.ru</td></tr><tr><td>Проверил</td><td>Корепанов</td><td></td><td></td><td></td><td></td></tr><tr><td>Н.контр.</td><td>Агафонов</td><td></td><td></td><td></td><td></td></tr></table>																								Изм.	Кол.уч.	Лист	№ док.	Подп.	Дата	Строительство водогрейной котельной 400Гкал/час на территории Ивановской ТЭЦ-2	Стадия	Лист	Листов							РД	246		Разработал	Чураков				07.25	Схема электрическая se0007: Е1ЕКГ01СТ101, Е1ЕКА01СТ101	ООО НПП "ЭСН" www.nppesn.ru			Проверил	Корепанов					Н.контр.	Агафонов				
Изм.	Кол.уч.	Лист	№ док.	Подп.	Дата	Строительство водогрейной котельной 400Гкал/час на территории Ивановской ТЭЦ-2	Стадия	Лист	Листов	
							РД	246	
Разработал	Чураков				07.25		Схема электрическая se0007: Е1ЕКГ01СТ101, Е1ЕКА01СТ101	ООО НПП "ЭСН" www.nppesn.ru	
Проверил	Корепанов	
Н.контр.	Агафонов	

Согласовано				
Инов. № подл.	Взамен инв. №			
	Подп. и дата			

Назначение	Давление на выходе ГРП-1 (13а)				Давление на входе ГРП-1 (14а)	Давление после заслонки №1 (11а)	Давление после заслонки №2 (12а)
KKS	E1EKG01CP001				E1EKA01CP001	E1EKD01CP001	E1EKD02CP001
Клеммник шкафа	ЩА сущ. ГРП-1 XT27 XT28 E1-A11-5B E1-A11-5A				ЩА сущ. ГРП-1 XT31 XT32 E1-A11-7B E1-A11-7A	ЩА сущ. ГРП-1 XT38 XT39 E1-A11-9B E1-A11-9A	ЩА сущ. ГРП-1 XT43 XT44 E1-A11-11B E1-A11-11A
Маркировка жил кабеля/провода							
Маркировка кабеля/провода	E1-6 МКЭШнг(А)-LS 3х0,75 Щкаф АСУ ГРП-1 (E1CJU01) L= Lg= Lt=				E1-7 МКЭШнг(А)-LS 3х0,75 Щкаф АСУ ГРП-1 (E1CJU01) L= Lg= Lt=	E1-8 МКЭШнг(А)-LS 3х0,75 Щкаф АСУ ГРП-1 (E1CJU01) L= Lg= Lt=	E1-9 МКЭШнг(А)-LS 3х0,75 Щкаф АСУ ГРП-1 (E1CJU01) L= Lg= Lt=
Маркировка жил кабеля/провода	XT1 15 16 17 E1-A11-5B E1-A11-5A PE				XT1 18 19 20 E1-A11-7B E1-A11-7A PE	XT1 21 22 23 E1-A11-9B E1-A11-9A PE	XT1 24 25 26 E1-A11-11B E1-A11-11A PE
Клеммник шкафа							
Маркировка провода							
Клеммники терминальной панели	A3.1 5B 5A Module TP-U				A3.1 7B 7A Module TP-U	A3.1 9B 9A Module TP-U	A3.1 11B 11A Module TP-U
Модуль ввода/вывода	CIDCS-6-3-0-3-3 XP1 M1234A-0				CIDCS-6-3-0-3-3 XP1 M1234A-0	CIDCS-6-3-0-3-3 XP1 M1234A-0	CIDCS-6-3-0-3-3 XP1 M1234A-0

						878.2023-АСУ ТП.СБ.2		
						РФ, Ивановская область, г.Иваново, ул. Суворова, 76		
Изм.	Кол.уч.	Лист	№ док.	Подп.	Дата	Строительство водогрейной котельной 400Гкал/час на территории Ивановской ТЭЦ-2	Стадия	Лист
							РД	247
Разработал	Чураков				07.25	Схема электрическая se0009: E1EKG01CP001, E1EKA01CP001, E1EKD01CP001, E1EKD02CP001	ООО НПП "ЭСН" www.nppesn.ru	
Проверил	Корепанов							
Н.контр.	Агафонов							

Согласовано	Прибор	Сигнализатор газов СТМ-10									
	KKS	E1UEN01CQ001									
	Клеммники шкафа	ЩА суш_ГРП-1 E1-S17-21 E1-S17-23									
	Маркировка жил кабеля/провода										
	Маркировка кабеля/провода	E1-30									
	Марка, тип, длина кабеля	КВВГнг(А)-LS 4х1,0 L= Lg= Lt=									
	Маркировка жил кабеля/провода	Шкаф АСУ ГРП-1 (E1CJU001) E1-S17-21 E1-S17-23									
	Клеммник шкафа	XT2 5 6									
	Ноль ~220В	N									
	Маркировка провода	A1 A2 K2-03 11 14 D1-B3 D1-B3 A1 A2 K2-04 11 14 D1-B4 D1-C4									

	Назначение			Неисправность шкафа сборки задвижек E1CDA01GH002		
	KKS			Сборка СЗ ГРП-1 (E1CDA01GH002)		
	Клеммники шкафа					
	Маркировка жил кабеля/провода					
	Маркировка кабеля/провода			E1-29		
	Марка, тип, длина кабеля			МКЭШвнг(А)-LS 1x2x0,75		
	Маркировка жил кабеля/провода			L=		
	Клеммник шкафа			Lg=		
	Плюс датчика 24В			Lt=		
	Минус датчика 24В					
Маркировка провода			Шкаф АСУ ГРП-1 (E1CJU01)			
Реле						
Маркировка провода						
Клеммники терминальной панели			A5.1 B5 C5			
Модуль ввода/вывода			Module TP-D			
			CIDC-6-3-0-3-3			
			XP1 M1252D-0			

Согласовано				
	Взамен инв. №			
	Подп. и дата			
	Инв. № подл.			

						878.2023-АСУ ТП.СБ.2			
						РФ, Ивановская область, г.Иваново, ул. Суворова, 76			
Изм.	Кол.уч.	Лист	№ док.	Подп.	Дата	Строительство водогрейной котельной 400Гкал/час на территории Ивановской ТЭЦ-2	Стадия	Лист	Листов
							РД	249	
Разработал	Чураков				07.25		Схема электрическая se0019: E1CDA01GH002		
Проверил	Корепанов					ООО НПП "ЭСН"			
Н.контр.	Агафонов					www.nppesn.ru			

Согласовано

Оборудование

KKS

Клеммник шкафа

Маркировка жил кабеля/провода

Маркировка кабеля/провода

Марка, тип, длина кабеля

Маркировка жил кабеля/провода

Клеммник шкафа

Маркировка провода

Реле

Маркировка провода

Клеммники терминальной панели

Описание сигнала

Модуль ввода/вывода

Дисковый затвор ГК-1
E1EKG12AA001

Сборка СЗ ГРП-1 (E1CDA01GH002)

5х1

2

5

7

8

11

14

18

19

20

21

25

E1-M7-A1

E1-M7-A5

E1-M7-A11

E1-M7-A12

E1-M7-A30

E1-M7-A19

E1-M7-A20

E1-M7-A6

E1-M7-A7

E1-M7-A8

E1-M7-A9

E1-M7-H1

E1-27

KBBГнг(A)-LS 19х1.0 (7р)

L=

Lg=

L=

Шкаф АСУ ГРП-1 (E1CJU01)

ХТ7

1

2

3

4

5

6

7

8

9

10

11

12

E1-M7-A1

E1-M7-A5

E1-M7-A11

E1-M7-A12

E1-M7-A19

E1-M7-A20

E1-M7-A9

E1-M7-A8

E1-M7-A6

E1-M7-A30

E1-M7-A7

E1-M7-H1

11

12

11

14

11

14

A1

A2

11

14

A1

A2

11

14

A1

A2

11

14

A1

A2

K7-10

K7-03

K7-04

K7-01

K7-02

K7-06

K7-07

K7-05

A1

A2

A1

A2

A1

A2

A1

A2

A1

A2

A1

A2

A1

A2

A1

A2

DO1-11B

DO1-11A

DO1-12B

DO1-12A

DO1-13B

DO1-13A

DI1-B18

DI1-C18

DI1-B19

DI1-C19

DI1-B20

DI1-C20

DI1-B21

DI1-C21

DI1-B22

DI1-C22

A6.1

11B

11A

12B

12A

13B

13A

A5.1

B18

C18

B19

C19

B20

C20

B21

C21

B22

C22

Module

Терминальная панель TP-O

Module

Терминальная панель TP-D

Стоп

Открыт

Закреть

Открыт

Закреть

Готовность

Дистанционный режим работы

Превышение момента

CIDC-6-3-0-3-3

CIDC-6-3-0-3-3

XP1

M12510-0

XP1

M1252D-0

Согласовано

Взамен инв. №

Подп. и дата

Инв. № подл.

878.2023-АСУ ТП.СБ.2

РФ, Ивановская область, г.Иваново, ул. Суворова, 76

Изм.

Кол.уч.

Лист

№ док.

Подп.

Дата

Строительство водогрейной котельной 400Гкал/час на территории Ивановской ТЭЦ-2

Стадия

Лист

Листов

РД

252

Разработал

Чураков

Проверил

Корепанов

Н.контр.

Агафонов

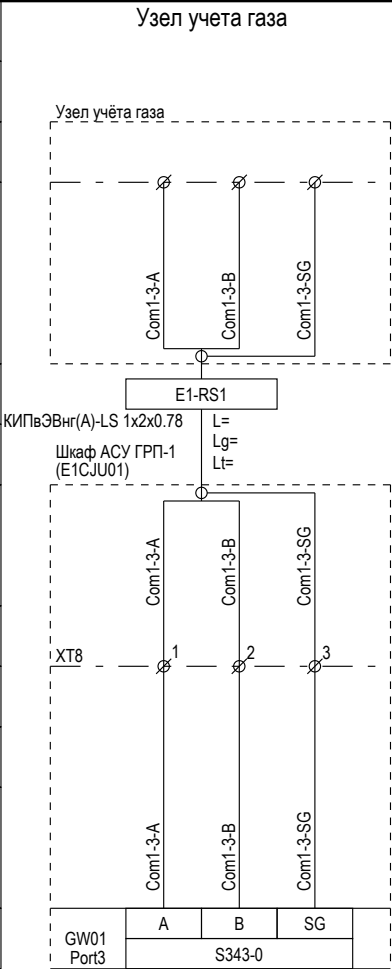
07.25

Схема электрическая se0028: E1EKG12AA001

ООО НПП "ЭСН"
www.nppesn.ru

Согласовано				
Инд. № подл.	Подп. и дата		Взамен инв. №	

Назначение
KKS
Клеммники шкафа
Маркировка жил кабеля/провода
Маркировка кабеля/провода
Марка, тип, длина кабеля
Маркировка жил кабеля/провода
Клеммник шкафа
Плюс 24В
Минус 24В
Маркировка провода
Клеммник модуля ввода/вывода



						878.2023-АСУ ТП.СБ.2		
						РФ, Ивановская область, г.Иваново, ул. Суворова, 76		
Изм.	Кол.уч.	Лист	№ док.	Подп.	Дата	Строительство водогрейной котельной 400Гкал/час на территории Ивановской ТЭЦ-2	Стадия	Лист
							РД	253
								Листов
Разработал	Чураков			07.25	Схема электрическая se0020:	ООО НПП "ЭСН" www.nppesn.ru		
Проверил	Корепанов							
Н.контр.	Агафонов							

