

[illegible]

[illegible]

Исполнительный механизм
Назначение
KKS
Клеммники шкафа
Маркировка жил кабеля/провода
Маркировка кабеля/провода
Марка, тип, длина кабеля
Маркировка жил кабеля/провода
Клеммник шкафа
Маркировка провода
Клеммники терминальной панели
Модуль ввода/вывода

Силовой трансформатор Т-1


температура обмотки фаза а, высокая сторона		температура обмотки фаза в, высокая сторона		температура обмотки фаза с, высокая сторона		температура обмотки фаза а, низкая сторона		температура обмотки фаза в, низкая сторона		температура обмотки фаза с, низкая сторона		напряжение низкая сторона		напряжение высокая сторона		ток фаза а низкая сторона		ток фаза в низкая сторона		ток фаза с низкая сторона	
F0AAT01CY001		F0AAT01CY002		F0AAT01CY003		F0AAT01CY004		F0AAT01CY005		F0AAT01CY006		F0AAT01CY007		F0AAT01CY008		F0AAT01CY009		F0AAT01CY010		F0AAT01CY011	

Шкаф АСУ ЭТО (E3CU01)

температура обмотки фаза а, высокая сторона		температура обмотки фаза в, высокая сторона		температура обмотки фаза с, высокая сторона		температура обмотки фаза а, низкая сторона		температура обмотки фаза в, низкая сторона		температура обмотки фаза с, низкая сторона		напряжение низкая сторона		напряжение высокая сторона		ток фаза а низкая сторона		ток фаза в низкая сторона		ток фаза с низкая сторона	
A3.1		1B		1A		3B		3A		5B		5A		7B		7A		9B		9A	

Module


TP-U												TP-U											
CIDCS-6-3-0-3-3												CIDCS-6-3-0-3-3											
XP1												M1234A-0											

 						878.2023-АСУ ТП.СБ.1			
						РФ, Ивановская область, г.Иваново, ул. Суворова, 76			
Изм.	Кол.уч.	Лист	№ док.	Подп.	Дата	Строительство водогрейной котельной 400Гкал/час на территории Ивановской ТЭЦ-2	Стадия	Лист	Листов
							РД	279	
Разработал	Чураков				07.25	Схема электрическая se0038: F0AAT01	ООО НПП "ЭСН" www.nppesn.ru		
Проверил	Корепанов								
Н.контр.	Агафонов								

Согласовано

	Взамен инв. №	
	Подп. и дата	
Инв. № подл.		

Исполнительный механизм
Назначение
KKS
Клеммники шкафа
Маркировка жил кабеля/провода
Маркировка кабеля/провода
Марка, тип, длина кабеля
Маркировка жил кабеля/провода
Клеммник шкафа
Маркировка провода
Клеммники терминальной панели
Модуль ввода/вывода

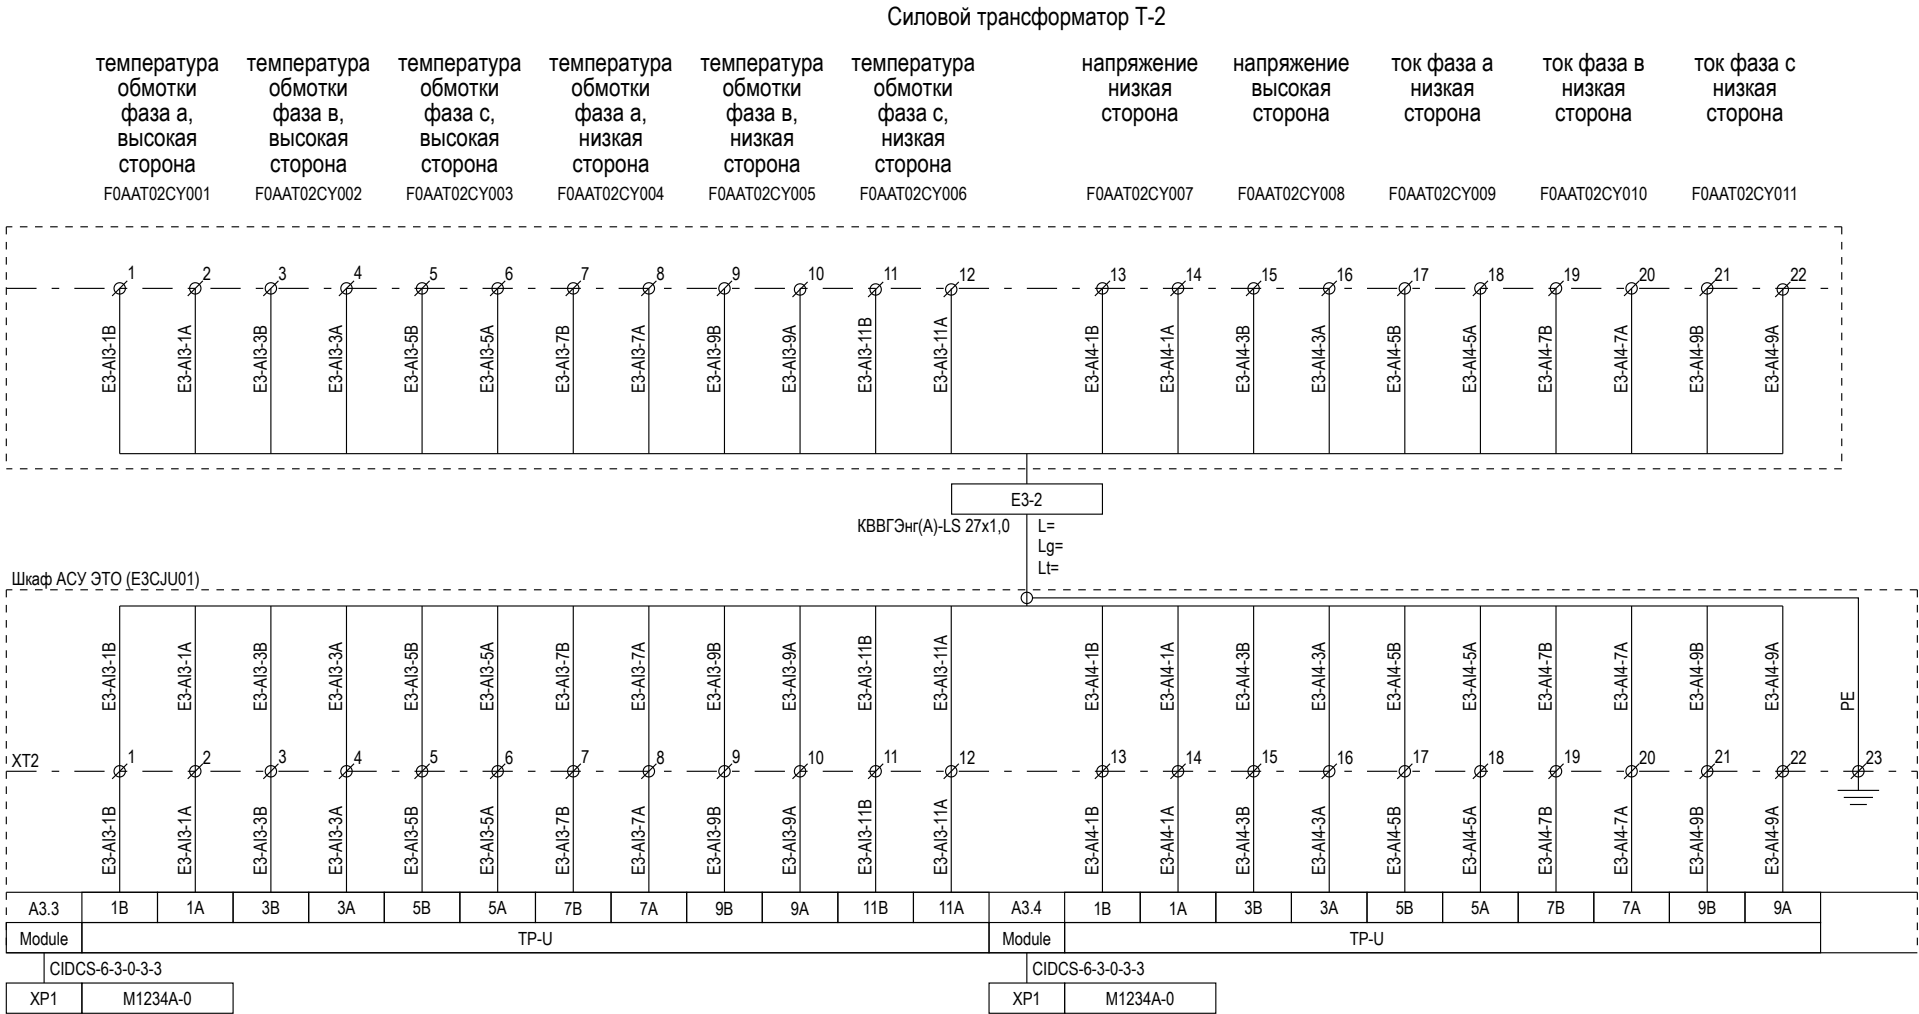

						878.2023-АСУ ТП.СБ.1			
						РФ, Ивановская область, г.Иваново, ул. Суворова, 76			
Изм.	Кол.уч.	Лист	№ док.	Подп.	Дата	Строительство водогрейной котельной 400Гкал/час на территории Ивановской ТЭЦ-2	Стадия	Лист	Листов
							РД	280	
Разработал	Чураков				07.25	Схема электрическая se0038: F0AAT02	ООО НПП "ЭСН" www.nppesn.ru		
Проверил	Корепанов								
Н.контр.	Агафонов								

Согласовано	</	
-------------	--	--	----	--

