


[illegible]

Согласовано

Исполнительный механизм
Назначение
KKS
Клеммники шкафа
Маркировка жил кабеля/провода
Маркировка кабеля/провода
Марка, тип, длина кабеля
Маркировка жил кабеля/провода
Клеммник шкафа
Маркировка провода
Клеммники терминальной панели
Модуль ввода/вывода

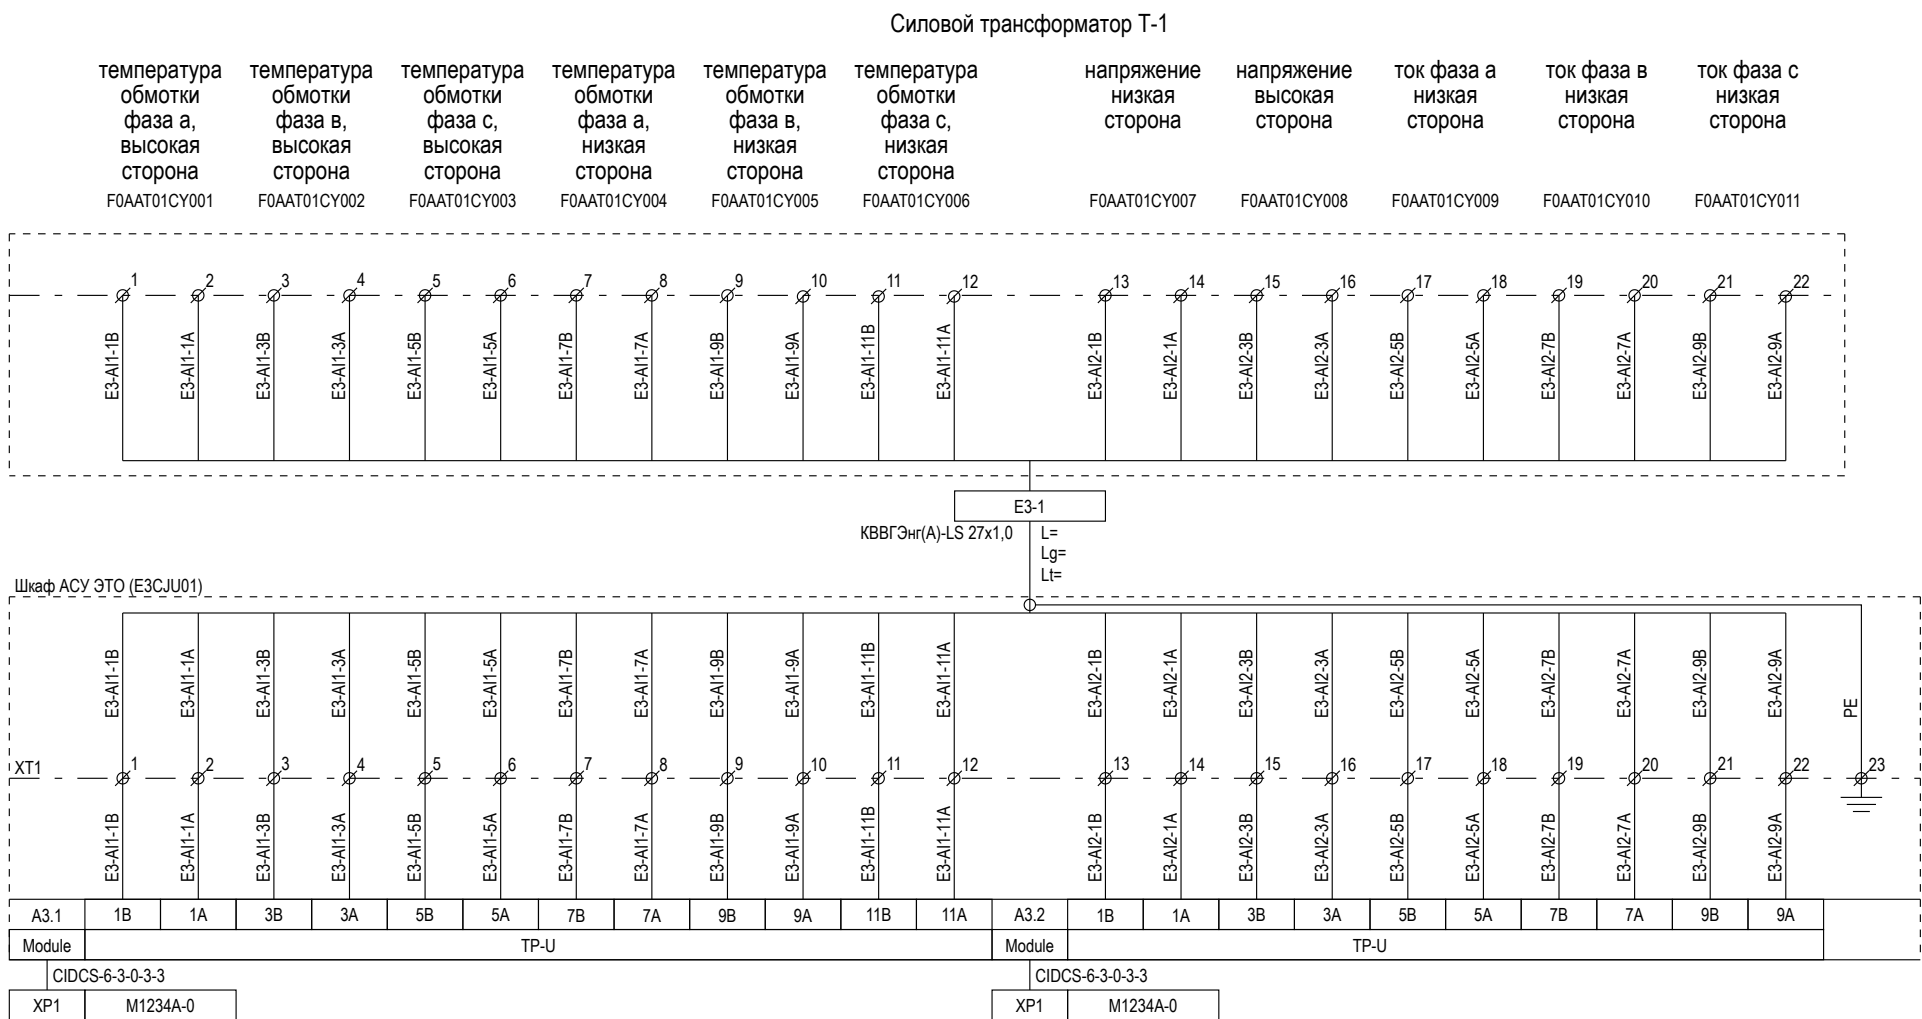


						878.2023-АСУ ТП.СБ.1			
						РФ, Ивановская область, г.Иваново, ул. Суворова, 76			
Изм.	Кол.уч.	Лист	№ док.	Подп.	Дата	Строительство водогрейной котельной 400Гкал/час на территории Ивановской ТЭЦ-2	Стадия	Лист	Листов
							РД	279	
Разработал	Чураков			07.25	Схема электрическая se0038: F0AAT01		ООО НПП "ЭСН" www.nppesn.ru		
Проверил	Корепанов								
Н.контр.	Агафонов								

Согласовано

	Взамен инв. №	
	Подп. и дата	
Инв. № подл.		

Исполнительный механизм
Назначение
KKS
Клеммники шкафа
Маркировка жил кабеля/провода
Маркировка кабеля/провода
Марка, тип, длина кабеля
Маркировка жил кабеля/провода
Клеммник шкафа
Маркировка провода
Клеммники терминальной панели
Модуль ввода/вывода

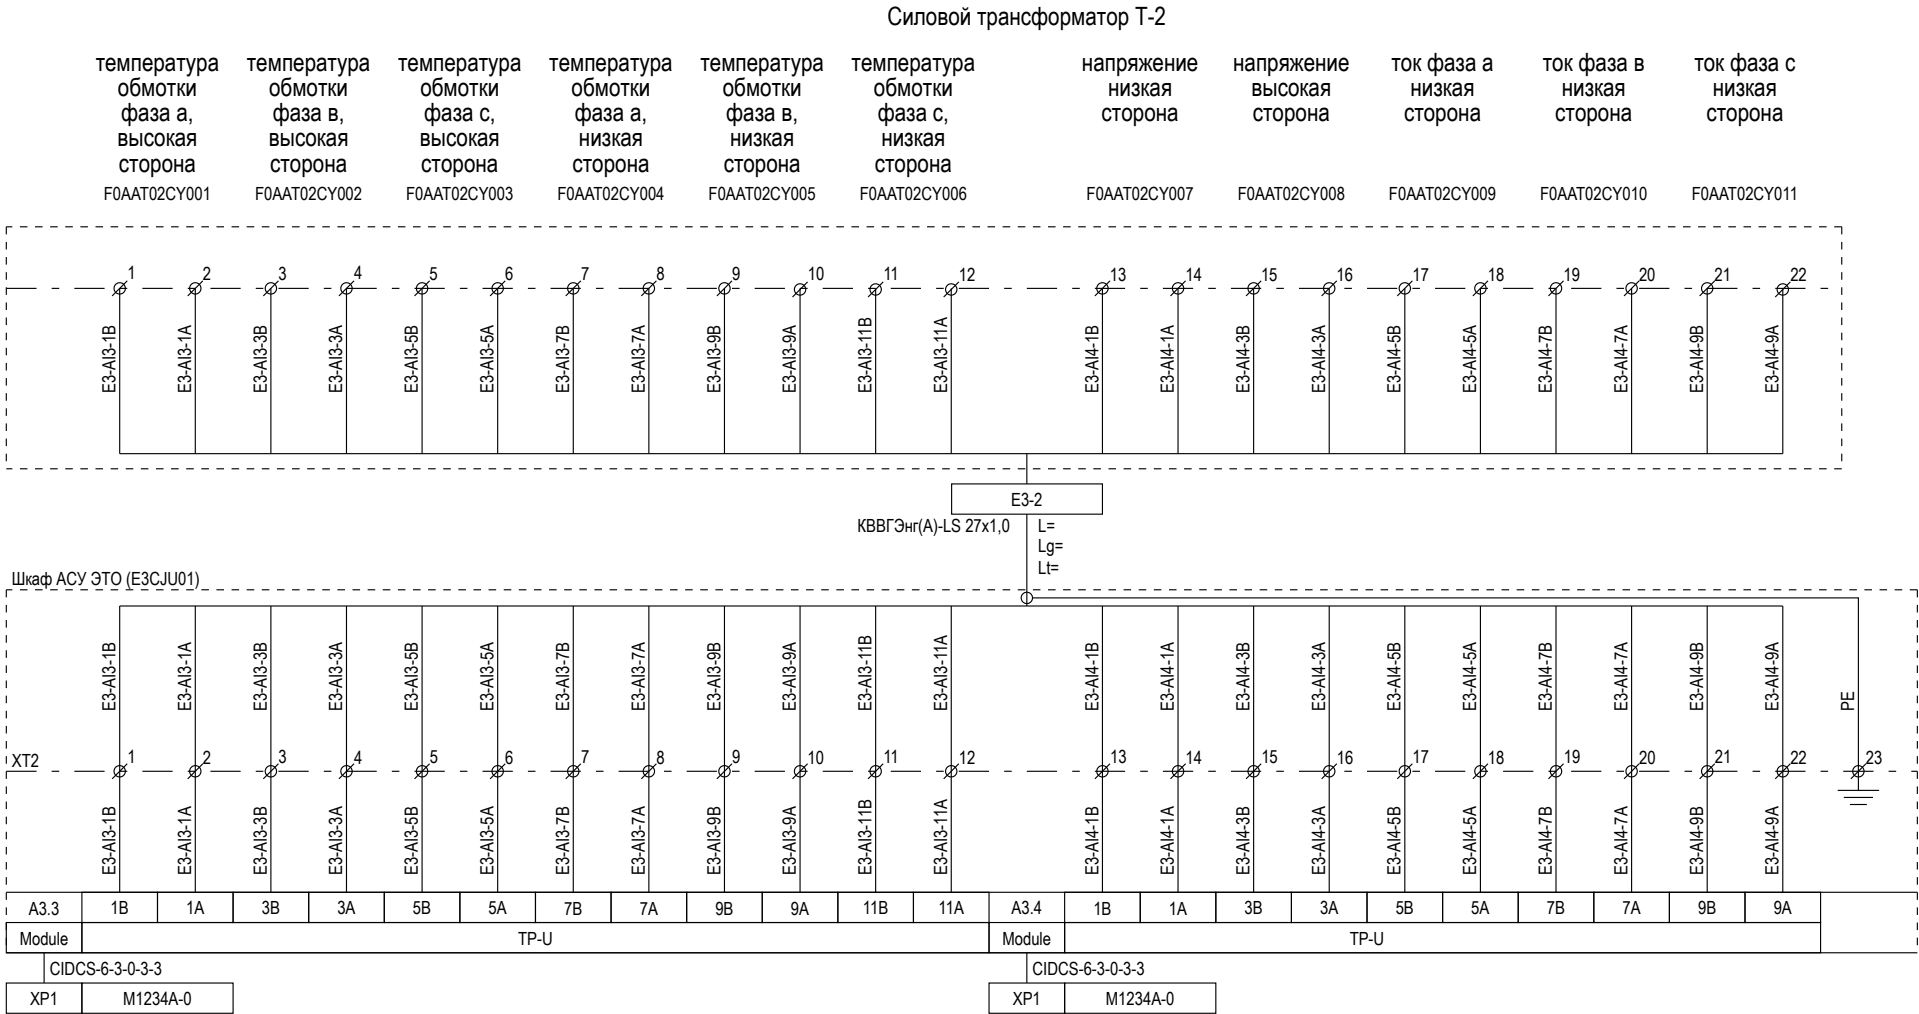

						878.2023-АСУ ТП.СБ.1			
						РФ, Ивановская область, г.Иваново, ул. Суворова, 76			
Изм.	Кол.уч.	Лист	№ док.	Подп.	Дата	Строительство водогрейной котельной 400Гкал/час на территории Ивановской ТЭЦ-2	Стадия	Лист	Листов
							РД	280	
Разработал	Чураков			07.25	Схема электрическая se0038: F0AAT02		ООО НПП "ЭСН" www.nppesn.ru		
Проверил	Корепанов								
Н.контр.	Агафонов								

[illegible]

Назначение	Сигналы с ячейки 5 (Ввод 1)		Сигналы с ячейки 8 (Ввод 2)		Сигналы с ячейки 1 (Ввод 1 к ТСН-35 2ТП-1000/6/0,4 кВ аккумулирующей насосной)		Сигналы с ячейки 2 (Ввод 1 к РУ-6 кВ здания расположения теплообменников)		Сигналы с ячейки 3 (Ввод 1 к Т-1 2ТП-3200/6/0,4 кВ здания РУСН)		Сигналы с ячейки 4 (Ввод к ТСН-1 здания РУСН)		Сигналы с ячейки 6 (секционный выключатель I с.ш. РУ-6 кВ)		Сигналы с ячейки 7 (секционный выключатель II с.ш. РУ-6 кВ)		Сигналы с ячейки 9 (Ввод к ТСН-2 здания РУСН)	
KKS	F0CBB05		F0CBB08		F0CBB01		F0CBB02		F0CBB03		F0CBB04		F0CBB06		F0CBB07		F0CBB09	
Клеммники шкафа																		
Маркировка жил кабеля/провода																		
Маркировка кабеля/провода																		
Марка, тип, длина кабеля																		
Маркировка жил кабеля/провода																		
Ethernet порт коммутатора																		
Назначение	Сигналы с ячейки 10 (Ввод 2 к Т-2 2ТП-3200/6/0,4 кВ здания РУСН)		Сигналы с ячейки 11 (Ввод 2 к РУ-6 кВ здания расположения теплообменников)		Сигналы с ячейки 12 (Ввод 2 к ТСН-36 2ТП-1000/6/0,4 кВ аккумулирующей насосной)													
KKS	F0CBB10		F0CBB11		F0CBB12													
Клеммники шкафа																		
Маркировка жил кабеля/провода																		
Маркировка кабеля/провода																		
Марка, тип, длина кабеля																		
Маркировка жил кабеля/провода																		
Ethernet порт коммутатора																		

						878.2023-АСУ ТП.СБ.1				
						РФ, Ивановская область, г.Иваново, ул. Суворова, 76				
Изм.	Кол.уч.	Лист	№ док.	Подп.	Дата	Строительство водогрейной котельной 400Гкал/час на территории Ивановской ТЭЦ-2		Стадия	Лист	Листов
								РД	281	
Разработал	Чураков				07.25	Схема электрическая se0039: F0CBB05, F0CBB08, F0CBB01, F0CBB02, F0CBB03, F0CBB04, F0CBB06, F0CBB07, F0CBB09, F0CBB10, F0CBB11, F0CBB12		ООО НПП "ЭСН" www.nppesn.ru		
Проверил	Корепанов									
Н.контр.	Агафонов									

